

GENERAL NOTES SECTIONS

A. CONCRETE & FOUNDATION DESIGN:

- ALL CONCRETE AND FOUNDATIONS ATTACHED TO THE HOST STRUCTURE SHALL HAVE A PRE INSPECTION.
- SOIL BEARING PRESSURE SHALL BE A MINIMUM OF 1500 PSF. THE BEARING CAPACITY OF THE SOIL TO BE VERIFIED BY A LICENSED CONTRACTOR PRIOR TO ANY POURING OF CONCRETE.
- ALL CONCRETE GRADE BEAMS AND FOOTINGS SHALL BE 3000 PSI MINIMUM.
- ALL SLABS ON GRADE SHALL BE A MINIMUM OF 4"THICK WITH FIBERMESH OR WIREMESH REINFORCING.
- ALL OVER POUR CONCRETE FILLED SUPPORTED SLABS SHALL BE 3000 PSI MIN., 2" MIN. THICKNESS WITH EPOXY.
- THE CONCRETE SHALL CONFORM TO ASTM C94 FOR THE FOLLOWING:
  - OPC (PORTLAND CEMENT TYPE 1,- ASTM C 150).
  - AGGREGATES - #6 STONE , ASTM C 33 SIZE NO. 67 LESS THAN 3/4".
  - AIR ENTRAINING +/- 1% - ASTM C 260.
  - WATER REDUCING AGENT - ASTM C 494.
  - CLEAN POTABLE WATER.
  - OTHER ADMIXTURES SHALL NOT BE PERMITTED.
- FIBERMESH REINFORCEMENT TO BE 3000 PSI (3/4" PER CUBIC YARD MIN.) AND MEET APPROPRIATE ACI AND ASTM REQUIREMENTS.
- METAL BARS SHALL CONFORM TO ASTM A 185.
- ALL REINFORCING SHALL CONFORM TO ASTM A615,BE GRADE 60 (60 KSI MIN.) DEFORMED BARS, #3 BARS MAY BE GRADE 40.
- PREPARE & PLACE CONCRETE ACCORDING TO AMERICAN CONCRETE INSTITUTE MANUAL STANDARD PRACTICE, PART 1, 2, & 3 ALONG WITH HOT WEATHER CONDITIONS RECOMMENDATIONS.
- IF UTILIZING EXISTING CONCRETE FOR FOUNDATION, CONCRETE SHALL BE A MINIMUM OF 4" IN THICKNESS, VISIBLY FREE OF ANY STRUCTURAL EXCESSIVE CRACKING, SPALLING OR OTHER DETERIORATION.
- CONTRACTOR TO FIELD VERIFY ANY EXISTING FOUNDATIONS NOTED ON SHEET S-1, DESIGN DATA: NOTE 10.
- DRY PACKING/POURING** IS NOT PERMITTED
- ALL REBAR REINFORCEMENT IN LINEAL AND ISOLATED FOOTINGS TO HAVE 3" OF CONCRETE COVER ON ALL SIDES. THIS DOES NOT INCLUDES SLABS.

B. MASONRY:

- CONCRETE MASONRY UNITS (CMU) SHALL BE STANDARD HOLLOW UNITS AND SHALL BE 2000 PSI MINIMUM BASED ON TYPE M OR S MORTAR.
- ALL MORTAR SHALL BE OF TYPE M OR S.
- ALL GROUT SHALL BE 2000 PSI MINIMUM AND HAVE MAXIMUM COARSE AGGREGATE SIZE OF 3/8".
- PROVIDE CLEAN-OUTS FOR REINFORCED CELLS CONTAINING REINFORCEMENT WHEN GROUT POUR EXCEEDS 5'-0" IN HEIGHT.

C. ALUMINUM:

- ALL STRUCTURAL ALUMINUM SHALL CONFORM TO THE MINIMUM REQUIREMENTS OF 6005-T5 FOR ALLOY WITH A MINIMUM THICKNESS OF 0.040" FOR SUPPORTING MEMBERS.
- ALL PLATES, ANGLES, AND CHANNELS SHALL BE 6005 T5 OR T6 ALLOY.
- WHERE KICK PLATES ARE USED A MINIMUM THICKNESS OF 0.024" SHALL APPLY.
- STRUCTURAL ALUMINUM DESIGN CONFORMS TO "PART 1-A - SPECIFICATIONS FOR ALUMINUM STRUCTURES - ALLOWABLE STRESS DESIGN" OR "PART 1-B - SPECIFICATIONS FOR ALUMINUM STRUCTURES - BUILDING LOAD AND RESISTANCE FACTOR DESIGN" OF THE ALUMINUM DESIGN MANUAL PREPARED BY THE ALUMINUM ASSOCIATION, INC.WASHINGTON D.C. FLORIDA BUILDING CODE EIGHTH EDITION (2023), BUILDING (CHAPTER 16 STRUCTURAL DESIGN & CHAPTER 20 ALUMINUM).
- WHERE ALUMINUM COMES INTO CONTACT WITH STEEL, OR PRESSURE TREATED LUMBER PROVIDE DIELECTRIC SEPARATION.
- ALUMINUM SELF MATING BEAM MEMBERS SHALL BE STITCHED WITH NO LESS THAN #10 SMS 6" FROM THE ENDS AND 12" ON CENTER, IF USING #12 SPACING MAY BE 24" ON CENTER.

- VINYL AND ACRYLIC PANELS SHALL BE REMOVABLE. THEY SHALL BE IDENTIFIED WITH A DECAL ESSENTIALLY STATING "REMOVABLE PANEL SHALL BE REMOVED WHEN WIND SPEEDS EXCEED 75 MPH" . DECAL SHALL BE PLACED SO IT IS VISIBLE WHEN PANEL IS INSTALLED. VINYL AND ACRYLIC PANELS MAY NOT BE USED IN FLOOD ZONE A.
- 1"x2"x0.040" NON-STRUCTURAL MEMBERS SHALL BE ATTACHED TO HOST WITH 1/4"Ø X 1-3/4" EMBEDMENT & 24" O.C. MASONRY SCREW FOR CONCRETE & EQUIVALENT SIZE WOOD SCREW WHEN IN WOOD & #10X 1/2" EMBEDMENT SMS OR TEK SCREWS IN ALUMINUM MEMBERS TYPICAL.
- ALL 5",7", AND 9" GUTTERS SHALL BE STRUCTURAL GUTTERS

D. FASTENERS:

- ALL LAG BOLTS SHALL CONFORM TO STAINLESS STEEL TYPE 300 18-8, WITH STANDARD FLAT WASHER UNLESS MANUFACTURER GALVANIZES BOLTS SPECIFIES FOR USE WITH ACQ PRESSURE TREATED WOOD.
- HEX BOLTS HAS TO BE ASTM A 325, PLATED WITH STANDARD FLAT WASHERS AND NUTS.
- ALL CONCRETE SCREWS SHALL BE, SIMPSON, HILTI, RAWL, TAPCON, REDHEAD, DYNABOLT, PORTECT OR APPROVED EQUAL.
- ALL METAL TIES AND ASSOCIATED ACCESSORIES SHALL BE HOT DIPPED GALVANIZED.
- ALL LAG BOLTS SHALL HAVE A MINIMUM EMBEDMENT OF 8X BOLT DIAMETER INTO STRUCTURAL FRAMING (G=42 MIN.).
- LAG BOLTS AND SCREWS INTO WOOD FRAMING SHALL BE PROVIDED WITH PILOT HOLES HAVING A DIAMETER NOT GREATER THAN 70 PERCENT OF THE THREAD DIAMETER OF THE BOLT OR SCREW. ALL LAG BOLTS AND SCREWS SHALL BE INSERTED IN PILOT HOLES BY TURNING AND UNDER NO CIRCUMSTANCES BY DRIVING WITH A HAMMER.
- ALL EXPANSION ANCHORS SHALL BE DESIGNED IN ACCORDANCE WITH THE SPECIFIC MANUFACTURER'S REQUIREMENTS AND ALLOWABLE LOADS AND SHALL ONLY BE APPLIED IN CONDITIONS ACCEPTABLE TO MANUFACTURER. FASTENERS SHALL BE A MINIMUM OF SAE GRADE #5 OR BETTER ZINC PLATED.
- ALL FASTENERS CONNECTING ALUMINUM COMPONENTS OR PRESSURE TREATED LUMBER ARE STAINLESS STEEL TYPE 300 18-8, UNLESS MANUFACTURER GALVANIZED BOLTS SPECIFIES FOR USE WITH ACQ PRESSURE TREATED WOOD, OR OTHERWISE NOTED ON PLANS.
- ALL FASTENERS SHALL COMPLY WITH ASTM A153.
- ALL CONNECTORS SHALL COMPLY WITH ASTM A653 CLASS G-185.
- FOR SMS, THE MINIMUM CENTER-TO-CENTER SPACING SHALL BE 3/4" AND MINIMUM CENTER-TO-EDGE SHALL BE 1/2" UNLESS NOTED OTHER WISE.

E. REFERENCE STANDARDS: (CURRENT EDITIONS OF)

ASTM E 119  
ASTM E 1300  
ASCE 7  
ALUMINUM DESIGN MANUAL-AA ASM35, AND SPEC. FOR ALUMINUM PART 1-A, & 1-B  
ASTM C94  
ASTM C150  
ASTM C33  
ASTM C260  
ASTM C494  
ASTM A615  
ASTM A185  
FLORIDA BUILDING CODE EIGHTH EDITION (2023), BUILDING  
FLORIDA BUILDING CODE EIGHTH EDITION (2023), RESIDENTIAL  
FLORIDA BUILDING CODE EIGHTH EDITION (2023), EXISTING  
HUD CODE

F. ABBREVIATIONS:

THE FOLLOWING LIST OF ABBREVIATIONS IS NOT INTENDED TO REPRESENT ALL THOSE USED ON THESE DRAWINGS, BUT TO SUPPLEMENT THE MORE COMMON ABBREVIATIONS.

- TYP -- TYPICAL
- SIM -- SIMILAR
- UON -- UNLESS OTHERWISE NOTED
- CONT -- CONTINUOUS
- VIF -- VERIFY IN FIELD

- SMB -- SELF MATING BEAM
- FSM -- FLORIDA SALES AND MARKETING
- REC -- RECEIVING CHANNEL

G. RESPONSIBILITY:

- ALL SITE WORK SHALL BE PERFORMED BY A LICENSED CONTRACTOR IN ACCORDANCE WITH APPLICABLE BUILDING CODES, LOCAL ORDINANCES, ETC.
- CONTRACTOR SHALL VERIFY ALL DIMENSIONS AND DETAILS, NOTIFYING ENGINEER OF ANY DISCREPANCIES BETWEEN DRAWINGS, FABRICATED ITEMS, OR ACTUAL FIELD CONDITIONS.
- ALL DETAILS ON THESE DRAWINGS ARE ENGINEERED BASED ON INFORMATION PROVIDED BY THE CONTRACTOR AND/OR MANUFACTURER.
- ANY DETAILS NOT SHOWN ARE TO BE ENGINEERED BY A LICENSED P.E. IN ACCORDANCE WITH STANDARD ENGINEERING PRACTICES.
- WHEN ATTACHING TO FASCIA, THE HOST STRUCTURE SHALL HAVE AT LEAST A 2"x4" FASCIA AND ROOF TRUSS SYSTEM. CONTRACTOR SHALL VERIFY THIS AND IF SMALLER, CONTRACTOR SHALL BRING STRUCTURE UP TO A 2"x4" FASCIA AND ENSURE LESS THAN A 2'-0" OVERHANG.
- FBC PLANS & ENGINEERING SERVICES INC. DOES NOT WARRANT, EITHER EXPRESSLY OR IMPLIED, THE QUALITY OF THE CONSTRUCTION, AND IS NOT RESPONSIBLE FOR THE INTERPRETATION OF DESIGNS AND END USE BY THE CLIENT/CONTRACTOR.
- CONTRACTOR TO VERIFY FEMA FLOOD ZONE OF THE PROPOSED STRUCTURE LOCATION TO ENSURE STRUCTURE IS NOT WITHIN SPECIAL FLOOD HAZARD AREAS.
- MISCELLANEOUS:**
  - ALUMINUM ADDITIONS ARE NOT TO BE INSTALLED ON A MANUFACTURED HOME, TRAILER HOME, OR PRE-FAB HOME. IF NO HOST BEAM IS PRESENT, A SEPARATE 4TH WALL SUPPORT SYSTEM MUST BE ENGINEERED TO ENSURE NO ADDITIONAL LOADING IS PLACED ON THE MANUFACTURED HOME.
  - IF ENCLOSURE CONTAINS A SWIMMING POOL OR SPA, THE ENCLOSURE SHALL COMPLY WITH RESIDENTIAL SWIMMING BARRIER REQUIREMENTS OF FLORIDA BUILDING CODE EIGHTH EDITION (2023), RESIDENTIAL R 4501.17 IN ITS ENTIRETY.
  - DOOR LOCATIONS MAY BE DETERMINED IN THE FIELD BY CONTRACTOR.
  - IF PAVERS ARE UNDER ALUMINUM MEMBERS THEY SHALL HAVE EPOXY ADHESIVE TO CONCRETE OR IF USING GROUT, ENSURE BONDING AGENT IS USED FIRST AND ADHERED WITH MINIMUM 3000 PSI GROUT.
  - SCREENING MATERIAL SHALL BE 18X14X0.013 OR EQUIVALENT DENSITY SCREEN MESH ONLY UNLESS NOTED ON DRAWING S-2.
  - ALL STRUCTURAL POST SHALL BE ANCHORED TO AN EXISTING/PROPOSED CONCRETE FOUNDATION FOR UPLIFT PURPOSES.
  - CONTRACTOR TO ENSURE ALL PROPOSED GUTTERS HAVE A POSITIVE FLOW.
  - EMERGENCY ESCAPE & RESCUE OPENING PER FBC R310.1 SHALL BE VERIFIED BY CONTRACTOR & BUILDING OFFICIAL.
  - ENCLOSED ADDITIONS TO MANUFACTURED HOMES SHALL NOT CHANGE THE EXIT FACILITIES FOR EGRESS PER HUD 3280.105, (A) THROUGH (A)(2)(IV), SO THAT THE DISTANCE TO EXIT DIRECTLY OUTSIDE FROM ALL BEDROOMS IS LESS THAN 35', AND, SO THAT TWO EXITS DIRECTLY OUTSIDE ARE STILL MAINTAINED. A CARPORT OR SCREEN ROOM SHALL BE CONSIDERED AS OUTSIDE. NON-HABITABLE SUNROOMS OR HABITABLE LIVING SPACE MAY BE ADDED WHERE AN EXIT DOOR WAS LOCATED AS LONG AS A NEW EXIT DOOR IS ADDED AND MEETS THE REQUIREMENTS OF HUD 3280.105.
  - AWS CERTIFIED WELDER REQUIRED FOR ALL WELDING.

SCREEN ENCLOSURE

DESIGN DATA: (SITE SPECIFIC DESIGN INFORMATION)

- ULTIMATE DESIGN WIND SPEED Vult, (3 SECOND GUST): 135 MPH  
NOMINAL DESIGN WIND SPEED Vasd: 105 MPH
- RISK CATEGORY: 1
- WIND EXPOSURE: C
- WIND LOADS:

|                          |        |
|--------------------------|--------|
| SCREEN ROOF:             | 10 PSF |
| SCREEN WALLS (WINDWARD): | 35 PSF |
| SCREEN WALLS (LEEWARD):  | 28 PSF |
| SOLID ROOF:              | N/A    |
- FACTOR APPLIED TO SCREEN WIND LOADS FOR 18/14: 0.88  
FACTOR APPLIED TO SCREEN WIND LOADS FOR 20/20: 1.0  
MESH TYPE AND LOCATION SHOWN ON S-2  
FACTORS FOR OTHER SCREEN MESHES TO BE DETERMINED BY THE ENGINEER
- FACTOR APPLIED TO SCREEN WIND LOADS FOR ALLOWABLE STRESS DESIGN: 0.6
- LIVE LOAD:

|                                                                |
|----------------------------------------------------------------|
| 300 lb. VERTICAL DOWNLOAD ON PRIMARY SCREEN ENCLOSURE MEMBERS. |
| 200 lb. VERTICAL DOWNLOAD ON SCREEN ENCLOSURE PURLINS.         |
- SCREEN ROOF TYPE: MANSARD
- NON-SCREEN ROOF TYPE: N/A
- EXISTING LINEAL FOOTING W/ SLAB (MIN. 12"x12" LINEAL FOOTING W/ 4"SLAB) MEETS THE REQUIREMENTS TO RESIST THE UPLOADS FOR THE PROPOSED STRUCTURE.

ALUMINUM STRUCTURAL MEMBERS

HOLLOW SECTIONS

2 X 2:-----2" X 2" X 0.044"  
2 X 3:-----2" X 3" X 0.050"  
2 X 4:-----2" X 4" X 0.050"  
2 X 5:-----2" X 5" X 0.050"  
3 X 3:-----3" X 3" X 0.125"

OPEN BACK SECTIONS

1 X 2:-----1" X 2" X 0.040"  
1 X 3:-----1" X 3" X 0.045"

SNAP SECTIONS

2 X 2 SMS:-----2" X 2" X 0.045"  
2 X 3 SMS:-----2" X 3" X 0.072"  
2 X 4 SMS:-----2" X 4" X 0.045"  
3 X 3 SMS:-----3" X 3" X 0.090"

SELF MATING (SMB)


2 X 4 SMB:-----2" X 4" X 0.044" X 0.100"  
2 X 5 SMB:-----2" X 5" X 0.050" X 0.118"  
2 X 6 SMB:-----2" X 6" X 0.050" X 0.120"  
2 X 7 SMB:-----2" X 7" X 0.057" X 0.120"  
2 X 8 SMB:-----2" X 8" X 0.072" X 0.224"  
2 X 9 SMB:-----2" X 9" X 0.072" X 0.224"  
2 X 10 SMB:-----2" X 10" X 0.092" X 0.374"

TUBE SECTIONS

2 X 2:-----2" X 2" X 0.090"

INDEX NOTES DRAWING DETAILS DETAILS

S-1  
S-2  
S-3  
S-4

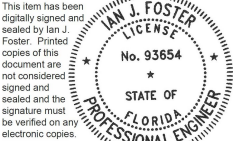

Digitally signed by  
Ian J Foster  
Date: 2026.06.10  
10:18:41 -04'00'

|   |  |  |  |
|---|--|--|--|
| PROFESSIONAL ENGINEER SEAL   |  |  |  |
| JOB NUMBER:<br><br>26_0605_339_GOYDA_REPLACEMC<br><br><br><br><br><br><br><br><br><br><br><br><br><br><br><br><br><br><br><br><br><br><br><br><br><br><br><br><br><br><br><br><br><br><br><br><br><br><br><br><br><br><br><br><br><br><br><br><br><br><br><br><br><br><br><br><br><br><br><br><br><br><br><br><br><br><br><br><br><br><br><br><br><br><br><br><br><br><br><br><br><br><br><br><br><br><br><br><br><br><br><br><br><br><br><br><br><br><br><br><br><br><br><br><br><br><br><br><br><br><br><br><br><br><br><br><br><br><br><br><br><br><br><br><br><br><br><br><br><br><br><br><br><br><br><br><br><br><br><br><br><br><br><br><br><br><br><br><br><br><br><br><br><br><br><br><br><br><br><br><br>10:18:48 -04'00'

PROFESSIONAL ENGINEER SEAL

|                                   |  |                               |  |                                                          |  |   |  |                                                              |  |                 |  |
|-----------------------------------|--|-------------------------------|--|----------------------------------------------------------|--|---|--|--------------------------------------------------------------|--|-----------------|--|
| <div>S-2</div> <div>DRAWING</div> |  | JOB NUMBER:                   |  | PROJECT<br>GOYDA<br>7325 CAYMAN CT<br>PALMETTO, FL 34221 |  | <div><p><b>FLORIDA</b><br/><b>Building</b><br/><b>Code</b></p><p><b>PLANS &amp; ENGINEERING SERVICE, INC</b></p></div> <div><b>FBC PLANS &amp; ENGINEERING SERVICES, INC.</b></div> |  | <div><b>FBC PLANS &amp; ENGINEERING SERVICES, INC.</b></div> |  | P. E. OF RECORD |  |
|                                   |  | 26_0605_339_GOYDA REPLACEMENT |  | DAVID W. SMITH<br>FL 53608                               |  |   |  |                                                              |  |                 |  |
|                                   |  | DRAW DATE: 06/08/2026         |  | THOMAS L. HANSON<br>FL 38654                             |  |   |  |                                                              |  |                 |  |
|                                   |  | REVISION 1:                   |  | IAN J. FOSTER<br>FL 93654                                |  |   |  |                                                              |  |                 |  |
|                                   |  | REVISION 2:                   |  | JOEL FALARDEAU<br>FL 70667                               |  |   |  |                                                              |  |                 |  |
| REVISION 3:                       |  |                               |  | ERIK STUART<br>FL 77605                                  |  |   |  |                                                              |  |                 |  |

**FOR WOOD:**  
(4) 1/4" LAG SCREWS @ 1-1/2" SPACING @ EA. GUTTER BRACKET & (1)1/4" LAG SCREWS @ 12" O.C. MAX. MINIMUM EMBEDMENT SHALL BE 2"

**FOR CONCRETE:**  
(3) 3/8" CONCRETE SCREWS @ 2" SPACING @ EA. GUTTER BRACKET & (1) 3/8" CONCRETE SCREWS @ 24" O.C. MAX. MINIMUM EMBEDMENT SHALL BE 2"

(1) 5", 7", OR 9"X 6" WIDTH X 0.072" MIN. EXTRUDED GUTTER BRACKET @ EA. BEAM & (1) GUTTER BRACKET BETWEEN BEAMS, ALL BRACKETS W/ (4) #12 X 3/4" SMS INTO GUTTER LIP

OPTIONAL 1" X 2" X 0.045" OPEN BACK W/ (2)#12 X 1-1/2" @ BEAM & AT GUTTER @ 24" O.C. (MAY USE 2X2 IN LIEU OF 1X2, USE #12 X 2-1/2" TEKS, SAME PATTERN APPLIES)

2" X 2" X 1/8" X ALUMINUM ANGLE w/ (4) #12 X 3/4" SMS INTO BEAM ON EA SIDE EA. LEG

2"X2"X0.062" RECEIVING CHANNEL W/ A MINIMUM OF (2) AND UP TO (4) #10X 3/4" EA SIDE TO COVER EXPOSED BEAM (NO MORE THAN 6" MAY BE CUT HORIZONTALLY)

2"X2" OR 2"X3"PURLIN (SEE S-2 FOR SIZE)

2" X 2" X 1/8" ALUMINUM ANGLE W/ (4) #12 X 3/4" SMS INTO PURLIN ON EA SIDE

5",7" OR 9" SUPER GUTTER

(4) #12 X 3/4" SMS INTO GUTTER EA SIDE

OPTIONAL Z-BRACKET 0.250"

OPTIONAL 1" X 2" X 0.045" OPEN BACK W/ (2)#12 X 1-1/2" @ BEAM & AT GUTTER @ 24" O.C. (MAY USE 2X2 IN LIEU OF 1X2, USE #12 X 2-1/2" TEKS, SAME PATTERN APPLIES)

NOTES:

- 2X4 SMB BEAM ONLY REQUIRES 4" WIDTH GUTTER BRACKET W/ (2) 3/8" LAGS
- FOR 9" SUPER GUTTER, AT THE PURLIN CONNECTION: USE 4" WIDTH GUTTER BRACKETS TYP

**A**

GUTTER BRACKET & BEAM ATTACHMENT DETAIL  
SCALE: N.T.S.

2" X \_PURLINS (SEE S-2 FOR SIZE) ATTACHED TO BEAM w/MIN (4) #10 X 1 1/2" SMS

ALUMINUM GUSSET PLATE (SEE CHARTS FOR SMS SIZE, QTY, AND PATTERN)

QTY. (B) #SMS

1/2" TYP

1/2" TYP

1/2" TYP

S3 PLATE WIDTH (SEE TABLE)

PLATE DEPTH (1" LESS BEAM DEPTD)

NOTES:

- TOTAL NUMBER OF SCREWS PER JOINT EQUALS 4 TIMES "B".
- PLATE WIDTH SHALL BE DETERMINED FROM ANGLE OF BEAM AND MINIMUM SPACE REQUIRED."S3" IS MINIMUM PLATE WIDTH.
- GUSSET PLATES CAN EXTERNAL OR INTERNAL.
- INTERNAL SCREWS FOR PURLIN CONNECTION MAY BE INCLUDED IN TOTAL NUMBER OF SCREWS.
- ALL** SPLICES WILL HAVE THE SAME PATTERN.
- ALL** SCREWS SHALL BE SPACED EQUALLY.
- DETAIL SHOWS 2X6SMB WITH 1/8" ALUMINUM GUSSET PLATE AS AN EXAMPLE.

| BEAM | GUSSET PLATE | SMS | "B"      | "S3" |
|------|--------------|-----|----------|------|
| 2X4  | 1/8"         | #12 | 9/18/36  | 16"  |
| 2X5  | 1/8"         | #12 | 9/18/36  | 16"  |
| 2X6  | 3/16"        | #12 | 9/18/36  | 16"  |
| 2X7  | 3/16"        | #12 | 10/20/40 | 18"  |
| 2X8  | 3/16"        | #12 | 14/28/56 | 18"  |
| 2X8  | 3/16"        | #14 | 12/24/48 | 18"  |
| 2X9  | 3/16"        | #14 | 14/28/56 | 20"  |
| 2X10 | 3/16"        | #14 | 15/30/60 | 20"  |

**B**

BEAM SPLICE GUSSET DETAIL  
SCALE: N.T.S.

2"X2"X0.62" RECEIVING CHANNEL W/ (4) #10X3/4" SMS EACH SIDE OF PURLIN & INTO CARRIER BEAM (MAY USE ANGLES EA SIDE)

PURLIN

2" X "SMB EAVE RAIL MEMBER (UNLESS OTHERWISE NOTED ON S-2) ATTACHED TO PURLIN W/ (2) #10 X 4" SMS THRU SCREW BOSS

1"X2"X0.045" OPEN BACK ATTACHED TO EAVE RAIL MEMBER #10X1-1/2" SMS @ 12" O.C

**C**

SLOPED OR FLAT PURLIN CONNECTION DETAIL  
SCALE: N.T.S.

ROOF BEAM (SLOPED OR FLAT)

CARRIER BEAM

2" X 2" X 0.125" ANGLE EA SIDE

1" X 2" MEMBER FOR SCREENING

#10 X 1-1/2" SMS @ 12" O.C. (MAX) CONNECTING 1" X 2" TO CARRIER BEAM

SEE TABLE BELOW FOR SCREW SIZE & AMOUNT (TYP EACH SIDE, EACH LEG)

| ROOF BEAM SIZE | 3/4" SMS PER SIDE PER LEG OF ANGLE | QTY. |
|----------------|------------------------------------|------|
| 2X4            | #12                                | 4    |
| 2X5            | #12                                | 5    |
| 2X6            | #12                                | 5    |
| 2X7            | #14                                | 6    |
| 2X8            | #14                                | 7    |
| 2X9            | #14                                | 8    |
| 2X10           | #14                                | 9    |

**D**

BEAM TO CARRIER BEAM CONNECTION DETAIL  
SCALE: N.T.S.

BOTH ENDS SIMILAR

1 1/2" x 8" x 1/8" ALUMINUM PLATE W/ (4) #14X 3/4" IN EAVE RAIL / CORNER BRACKET& BRACE

1 3/4"

STRAP INSIDE ROOF BRACE

CORNER PIECE MADE FROM 2X2X0.044 MATERIAL W/#12X2" EA SIDE

(4) #14 @ EAVE RAIL (2) @ CORNER PIECE (4)@ BRACE

**E**

ROOF BRACING CONNECTION DETAIL  
SCALE: N.T.S.

HINGE LOCATION

2" X 2" EXTRUSION

HINGE LOCATION

DOOR

HINGE LOCATION

2" X 2" EXTRUSION

**F**

TYPICAL SCREEN DOOR CONNECTION DETAIL  
SCALE: N.T.S.

NOTES:

- HINGES SHALL BE ATTACHED TO STRUCTURE W/ (3) #10 X 5/8" SMS MINIMUM.
- DOOR SHALL BE ATTACHED TO ENCLOSURE W/(2) HINGES MINIMUM.
- HINGES SHALL BE ATTACHED TO DOOR WITH (3)#10 X 5/8" SMS. FASTEN A 1" X 2" X 0.044" TO UPRIGHT W/#12 X 1" SMS @ 12" O.C. AND WITHIN 3" FROM END OF THE UPRIGHT(IF APPLICABLE).

This item has been digitally signed and sealed by Ian J. Foster. Printed copies of this document are not considered signed and sealed and the signature must be verified on any electronic copies.

IAN J. FOSTER  
LICENSE  
No. 93654  
STATE OF FLORIDA  
PROFESSIONAL ENGINEER

Digitally signed by Ian J Foster  
Date: 2026.06.10 10:18:53 -04'00'

PROFESSIONAL ENGINEER SEAL

|                |                  |               |                |             |          |
|----------------|------------------|---------------|----------------|-------------|----------|
| P.E. OF RECORD | FL 53608         | FL 38654      | FL 93654       | FL 70667    | FL 77605 |
| DAVID W. SMITH | THOMAS L. HANSON | IAN J. FOSTER | JOEL FALARDEAU | ERIK STUART |          |

**FBC PLANS & ENGINEERING SERVICES, INC.**

ADDRESS: 5344 9th Street Zephyrhills, FL 33542  
PHONE: (813)838-0735  
FAX: 1-(866)824-7894  
E-MAIL: erb@fbcplans.com  
WEBSITE: www.fbcplans.com  
C.O.A.: #29054

Florida Building Code  
PLANS & ENGINEERING SERVICES, INC.

**PROJECT**  
GOYDA  
7325 CAYMAN CT  
PALMETTO, FL 34221

**CONTRACTOR**  
REPLACE MY CAGE  
6301 PORTER ROAD UNIT 12  
SARASOTA, FL 34240

**JOB NUMBER:**  
26\_0605\_339\_GOYDA REPLACEMENT


DRAW DATE: 06/08/2026

REVISION 1:  
REVISION 2:  
REVISION 3:

DETAILS

**S-3**



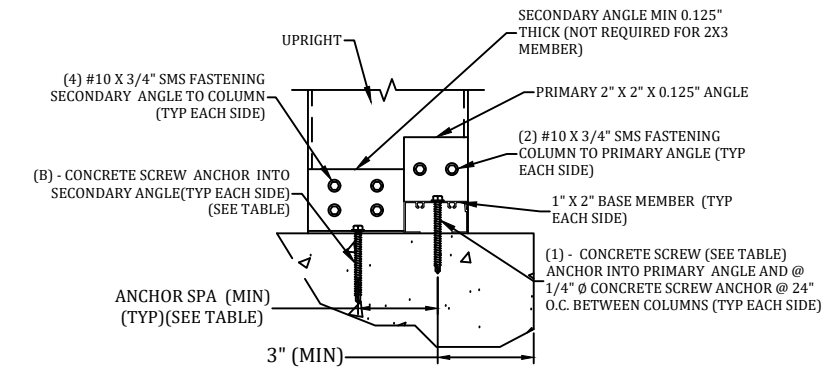


NOTES:

1. NUMBER OF ANCHORS "B" IS EACH SIDE INTO THE SECONDARY ANGLE AND DOES NOT INCLUDE THE ANCHOR INTO THE 1X2.
2. MINIMUM EMBEDMENT OF ANCHORS INTO CONCRETE FOOTING SHALL BE 2-3/4" AT ALL UPRIGHT LOCATIONS. ALL SCREW LENGTHS AT UPRIGHT CONNECTIONS SHALL BE OF SUFFICIENT LENGTH FOR REQUIRED EMBEDMENT INTO CONCRETE FOOTING WHEN A PAVER DECK IS PRESENT.
3. CONCRETE SCREW ANCHOR DESIGNS ARE BASED ON THOSE LISTED ON S-1, D. FASTENERS, OTHER BRAND & TYPE SHALL BE APPROVED BY ENGINEER.
4. 2X3W/1X2 CORNER POST SHALL REQUIRE SAME BASE CONNECTIONS AS 2X4 SHOWN IN TABLE.
5. IF FOR AN IN-FILL, TOP OF COLUMN CONNECTION SIMILAR IF CONCRETE LINTEL.
6. IF WOOD LINTEL/DECK, DOUBLE LEDGE REQUIRED (MIN. 3 5/8") MAY SUBSTITUTE LAG SCREW FOR LDT FOR BOTH PRIMARY & SECONDARY ANGLES.
7. 2X2X.045 DOOR JAMB MEMBER SHALL CONNECT SIMILAR TO 2X3 MEMBER.
8. SEE S-1, DESIGN DATA: NOTE 10 FOR FOUNDATION INFORMATION.


| COLUMN SIZE | 1/4" AND 3/8" Ø CONCRETE SCREW ANCHOR |                 |
|-------------|---------------------------------------|-----------------|
|             | "B"                                   | MINIMUM SPACING |
| 2X3-1/4"    | 0                                     | 0"              |
| 2X4-1/4"    | 1                                     | 2"              |
| 2X5-1/4"    | 1                                     | 2 1/2"          |
| 2X6-3/8"    | 1                                     | 3"              |
| 2X7-3/8"    | 1                                     | 3 1/2"          |
| 2X8-3/8"    | 2                                     | 3"              |
| 2X9-3/8"    | 2                                     | 3 1/2"          |
| 2X10-3/8"   | 2                                     | 4"              |

**G** 2" X 3" OR LARGER UPRIGHT TO CONCRETE W/WO PAVER  
DETAILS  
SCALE: N.T.S.

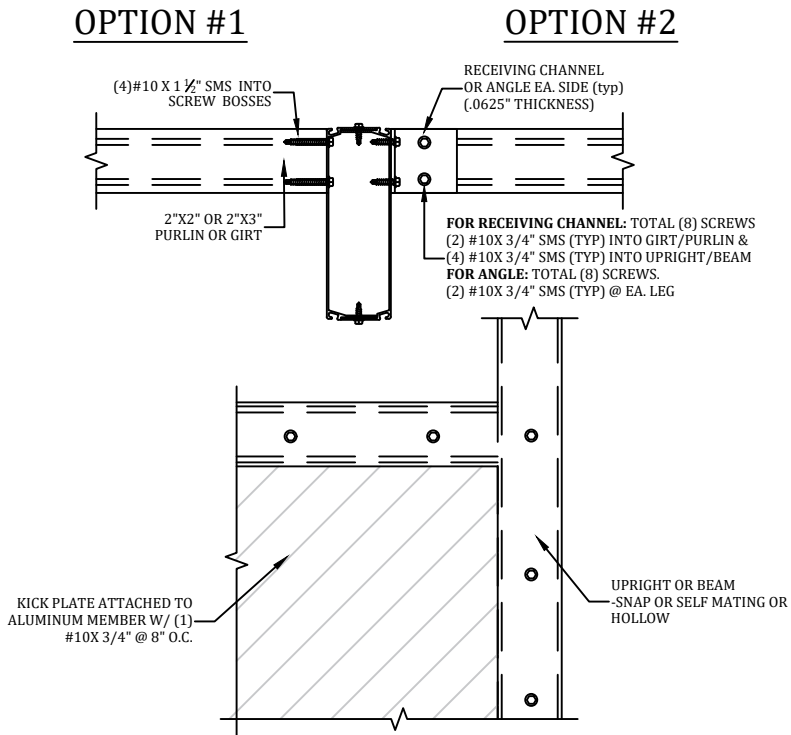


NOTES:  
1. KICK PLATE TO BE APPLIED TO UPRIGHT CHAIRRAIL OR GIRT IF APPLICABLE

**H** PURLIN OR GIRT TO BEAM OR POST DETAIL  
SCALE: N.T.S.

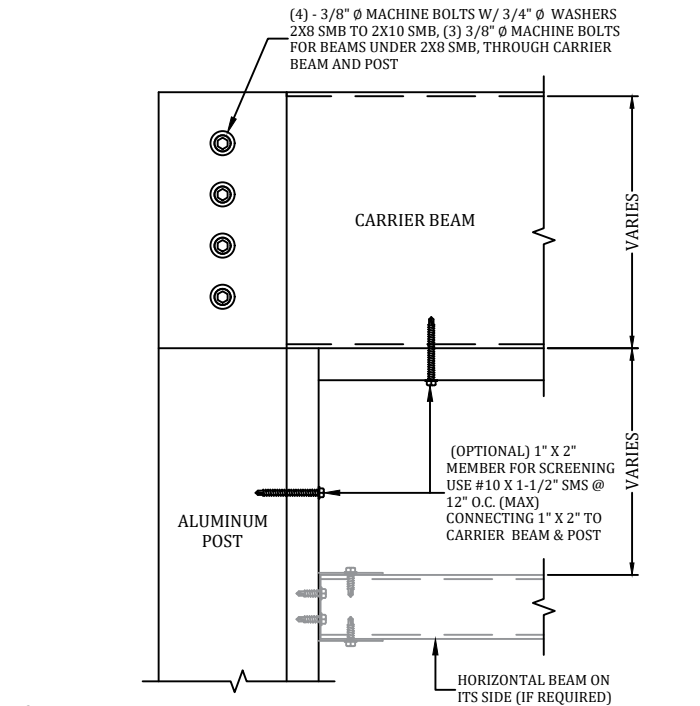


NOTE:  
1. PERPENDICULAR CARRIER BEAM: USE 0.125" RECEIVING CHANNEL WHICH WILL CONNECT TO THE POST W/(4) 3/8" THRU BOLTS USED FOR THE PRIMARY CARRIER BEAM, THEN USE (3) 3/8"Ø MACHINE BOLTS W/ 3/4"Ø WASHERS TO ATTACH THE PERPENDICULAR CARRIER BEAM TO THE RECEIVING CHANNEL.  
2. HORIZONTAL BEAM DETAIL WILL BE PROVIDED IF NEEDED.

**D1** BEAM TO POST DETAIL  
SCALE: N.T.S.

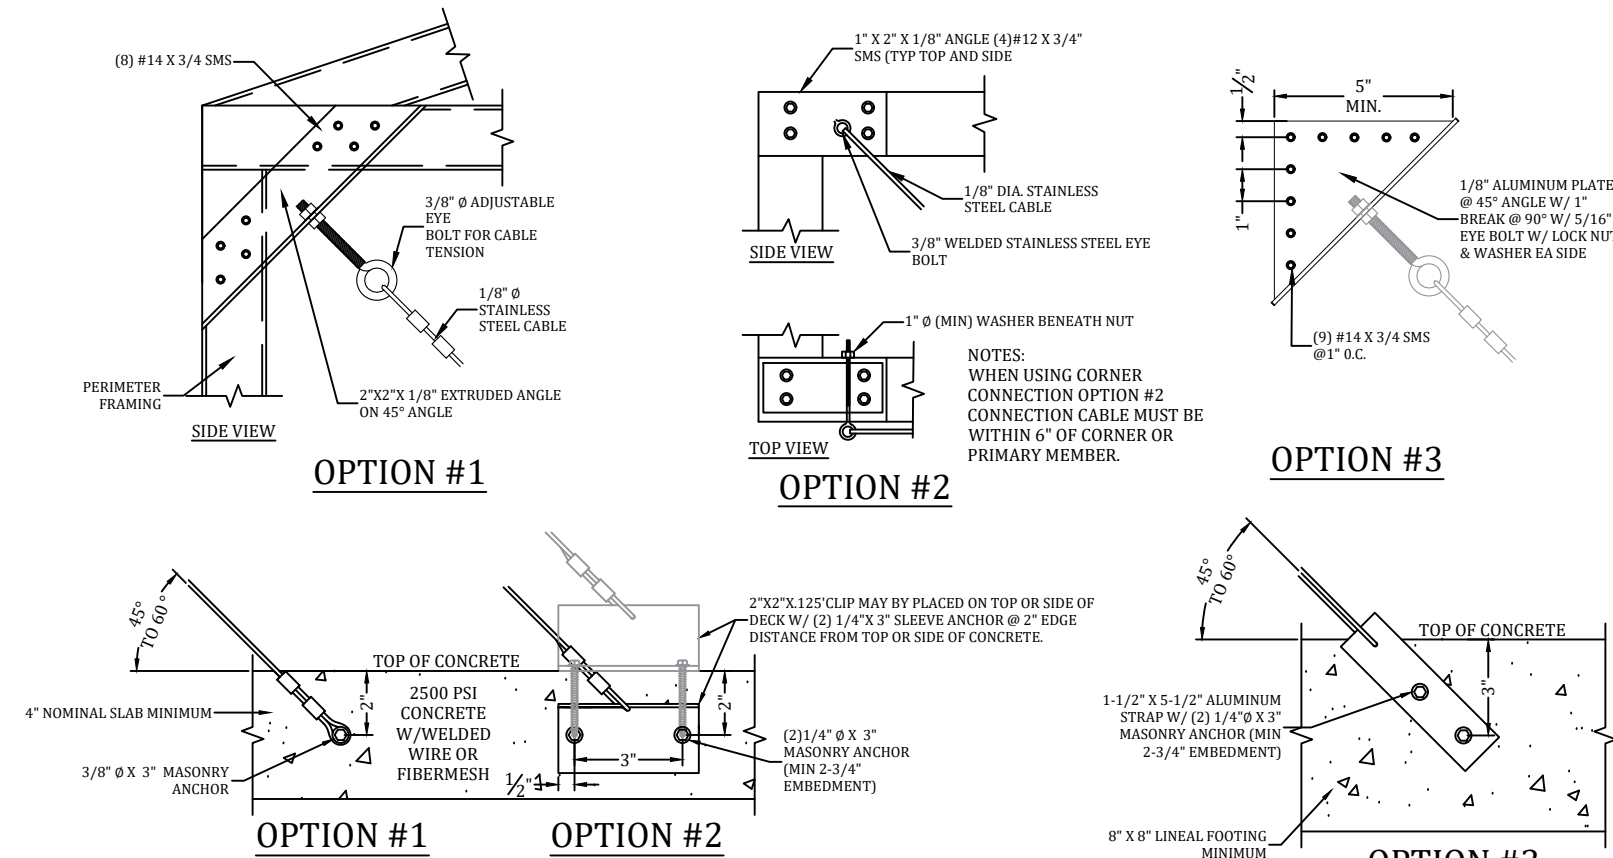


**J** CABLE CONNECTION AT CORNER AND FOUNDATION  
SCALE: N.T.S.

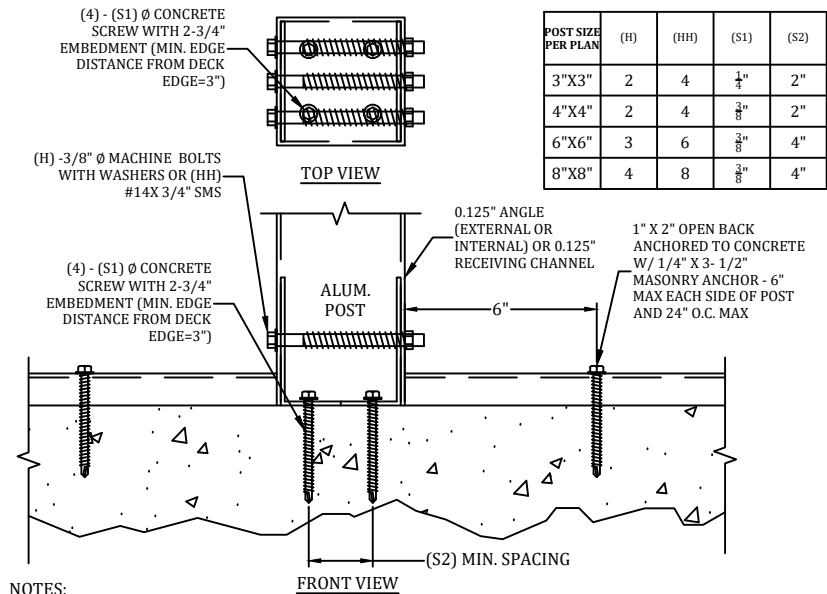

NOTES:  
1. CONCRETE SCREW ANCHOR DESIGNS ARE BASED ON TITEN HD (S1) Ø SCREW ANCHORS, OTHER SIZE OR TYPE OF ANCHORS SHALL NOT BE USED.  
2. FOR PATIO COVERS AND CARPORTS: DISREGARD THE 1X2 OPEN BACK SCREEN MEMBER ON THE FOUNDATION TYP.  
3. MINIMUM EMBEDMENT OF ANCHORS INTO CONCRETE FOOTING SHALL BE 2-3/4" AT ALL POST LOCATIONS. ALL SCREW LENGTHS AT POST CONNECTIONS SHALL BE OF SUFFICIENT LENGTH FOR REQUIRED EMBEDMENT INTO CONCRETE FOOTING WHEN A PAVER DECK IS PRESENT.  
4. MINIMUM EMBEDMENT OF ANCHORS INTO CONCRETE FOOTING SHALL BE 2-3/4" AT AT ALL UPRIGHT LOCATIONS. ALL SCREW LENGTHS AT UPRIGHT CONNECTIONS SHALL BE OF SUFFICIENT LENGTH FOR REQUIRED EMBEDMENT INTO CONCRETE FOOTING WHEN A PAVER DECK IS PRESENT.  
5. DETAIL MAY BE FLIPPED AS NEEDED  
6. USE 1/4" X 3" LAG SCREWS IN LIEU OF CONCRETE SCREWS FOR WOOD HEADERS, JOISTS, AND GIRDERS  
7. SEE S-1, DESIGN DATA: NOTE 10 FOR FOUNDATION INFORMATION.

**G1** ALUM. POST CONNECTION DETAIL  
SCALE: N.T.S.

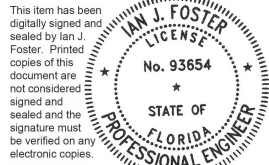

Digitally signed by Ian J Foster

Date: 2026.06.10 10:18:59 -04'00'

| P.E. OF RECORD |          | P.E. OF RECORD   |          | P.E. OF RECORD |          |
|----------------|----------|------------------|----------|----------------|----------|
| DAVID W. SMITH | FL 53608 | THOMAS L. HANSON | FL 38654 | IAN J. FOSTER  | FL 93654 |
| JOEL FALARDEAU | FL 70667 | ERIK STUART      | FL 77605 |                |          |

| ADDRESS:        |  | PHONE:        |  | FAX:            |  | E-MAIL:          |  | WEBSITE:         |  | C.O.A.: |  |
|-----------------|--|---------------|--|-----------------|--|------------------|--|------------------|--|---------|--|
| 5344 9th Street |  | (813)838-0735 |  | 1-(866)824-7894 |  | erb@fbcplans.com |  | www.fbcplans.com |  | #29054  |  |

|          |          |          |          |          |          |
|----------|----------|----------|----------|----------|----------|
| FL 33542 | FL 33542 | FL 33542 | FL 33542 | FL 33542 | FL 33542 |
|----------|----------|----------|----------|----------|----------|

| PROJECT                                       |  | CONTRACTOR                                                |  |
|-----------------------------------------------|--|-----------------------------------------------------------|--|
| GOYDA<br>7325 CAYMAN CT<br>PALMETTO, FL 34221 |  | REPLACE MY CAGE<br>6301 PORTER ROAD<br>SARASOTA, FL 34240 |  |

| JOB NUMBER:                   |  | REVISION 1: |  | REVISION 2: |  | REVISION 3: |  |
|-------------------------------|--|-------------|--|-------------|--|-------------|--|
| 26_0605_339_GOYDA REPLACEMENT |  | 06/08/2026  |  |             |  |             |  |

| DETAILS |  |
|---------|--|
| S-4     |  |