


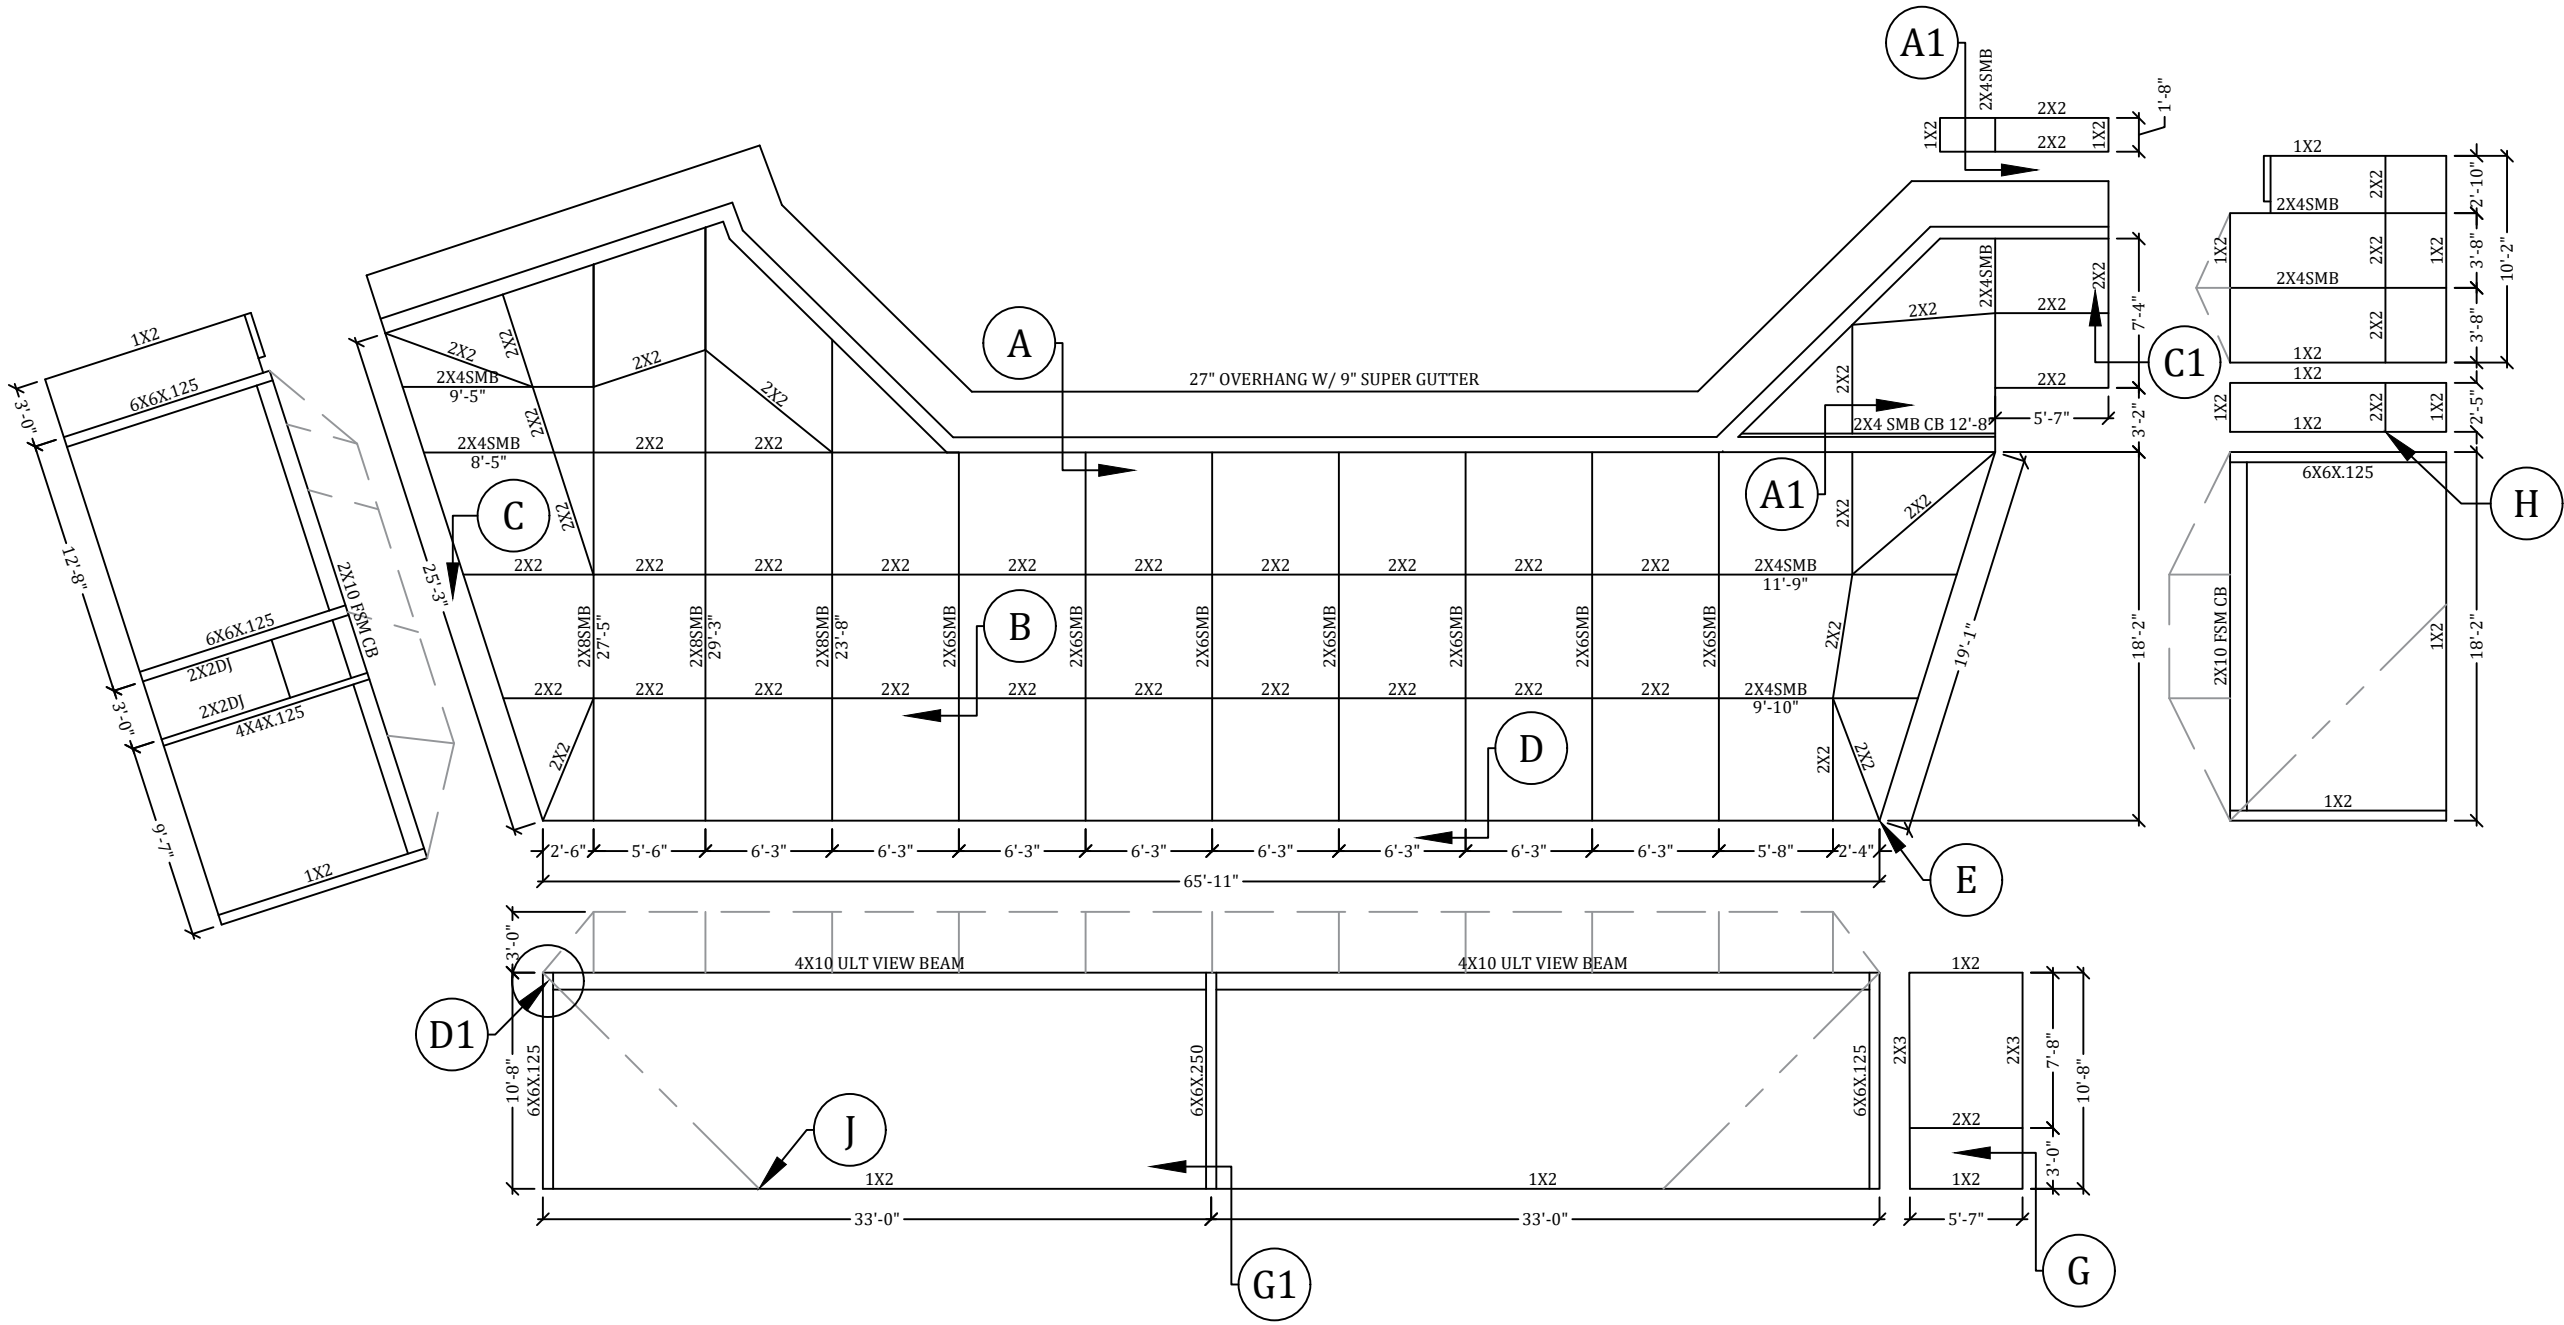

F

DOOR LOCATION MAY BE DETERMINED IN THE FIELD BY THE CONTRACTOR.

JOB NUMBER:
25_0902_192_LANDIS_REPLACMC

DRAW DATE: 09/08/2025

REVISION 1:

REVISION 2:

REVISION 3:

PROJECT
LANDIS
4129 HIGEL AVE
SIESTA KEY, FL 34242

CONTRACTOR
REPLACE MY CAGE
6301 PORTER ROAD UNIT 12
SARASOTA, FL 34240

DRAWING
S-2

FBC PLANS & ENGINEERING
SERVICES, INC.

P. E. OF RECORD

DAVID W. SMITH	FL 53608
THOMAS L. HANSON	FL 38654
IAN J. FOSTER	FL 93654
JOEL FALARDEAU	FL 70667
ERIK STUART	FL 77605

ADDRESS: 5344 9th Street
Zephyrhills, FL 33542


PHONE: (813)838-0735

FAX: 1-(866)824-7894

E-MAIL: erb@fbcplans.com


WEBSITE: www.fbcplans.com

C.O.A.: #29054

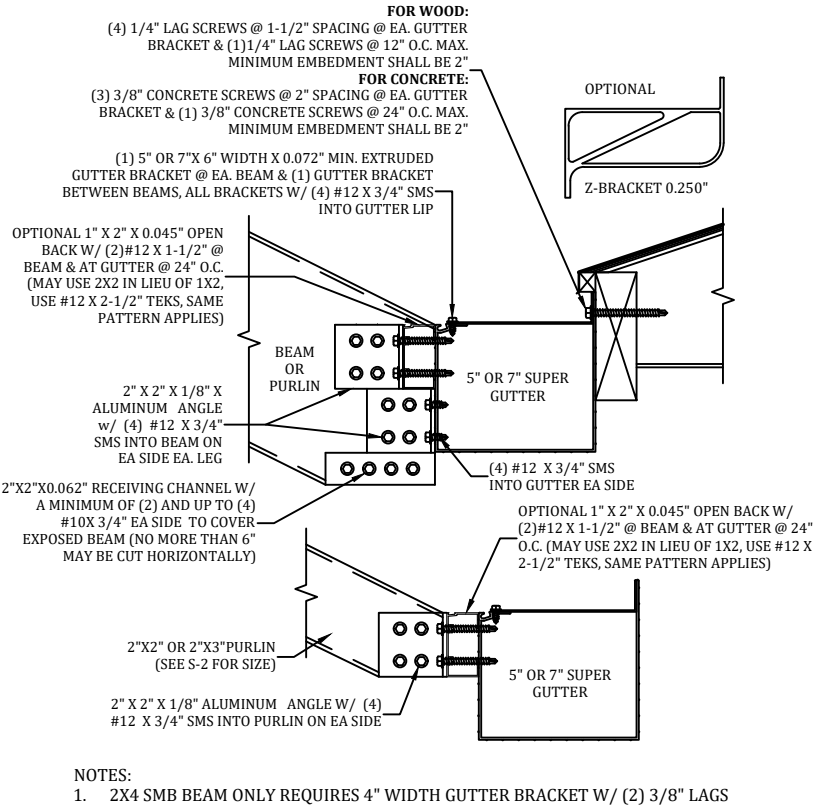


A

GUTTER BRACKET & BEAM ATTACHMENT DETAIL
SCALE: N.T.S.

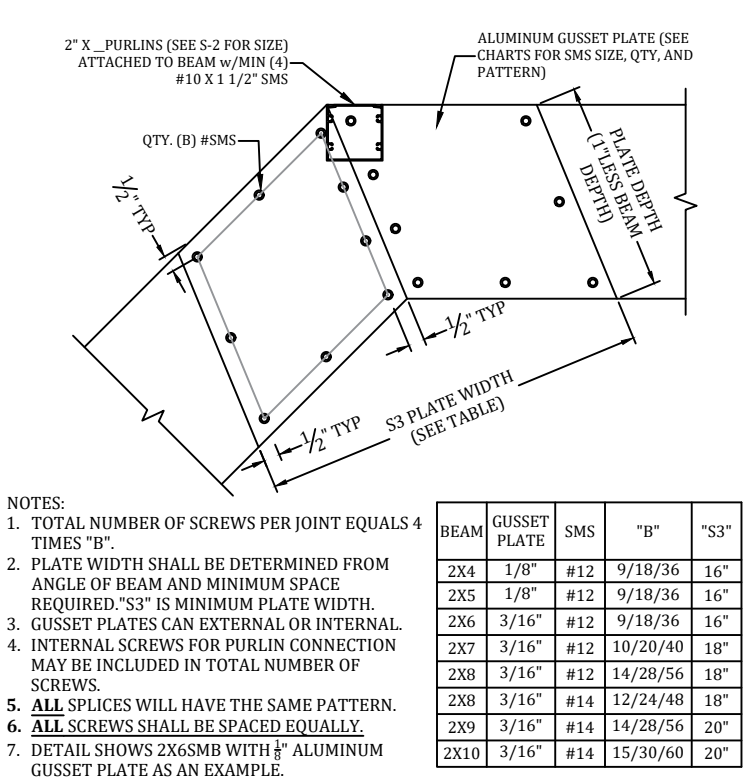


B

BEAM SPLICE GUSSET DETAIL
SCALE: N.T.S.

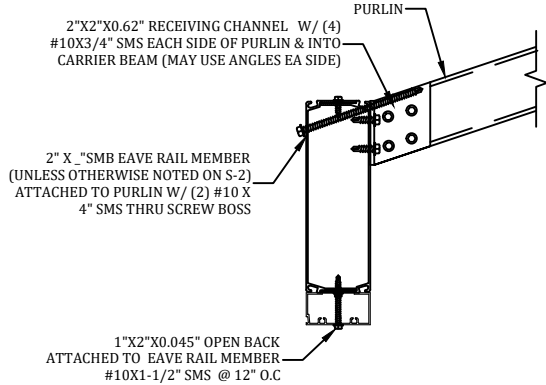


C

SLOPED OR FLAT PURLIN CONNECTION DETAIL
SCALE: N.T.S.

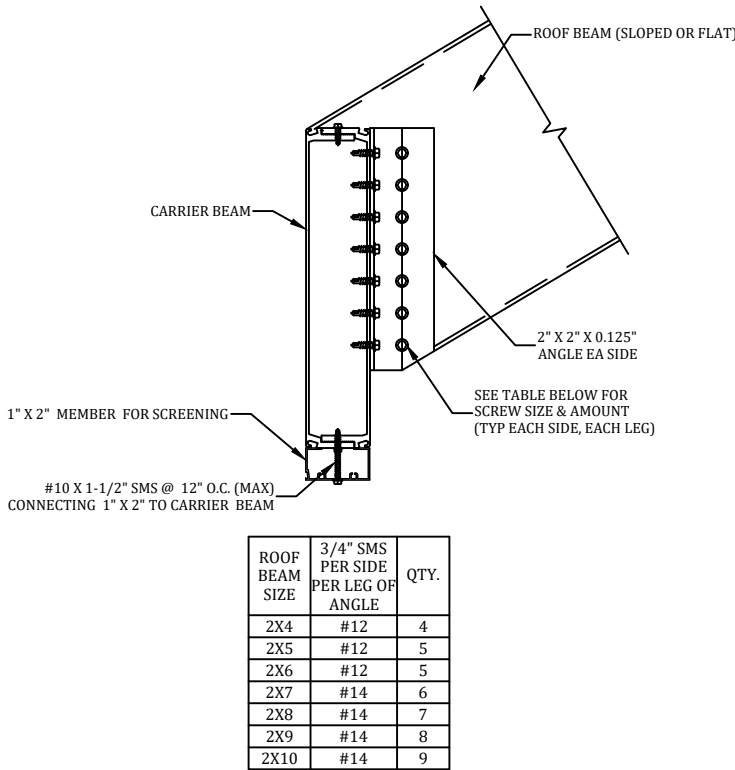


D

BEAM TO CARRIER BEAM CONNECTION DETAIL
SCALE: N.T.S.

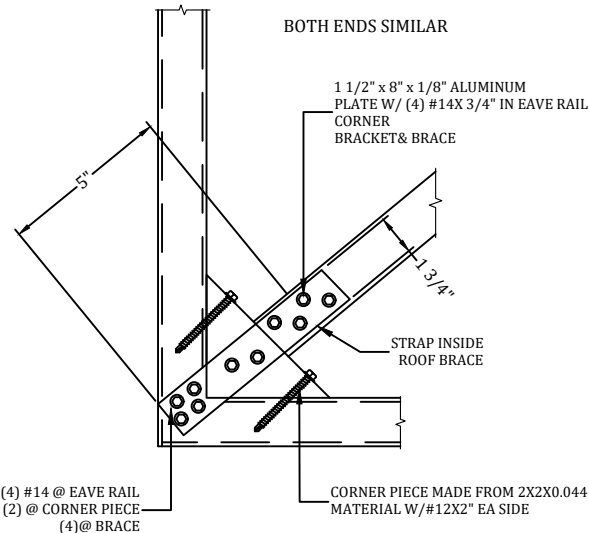

E

ROOF BRACING CONNECTION DETAIL
SCALE: N.T.S.

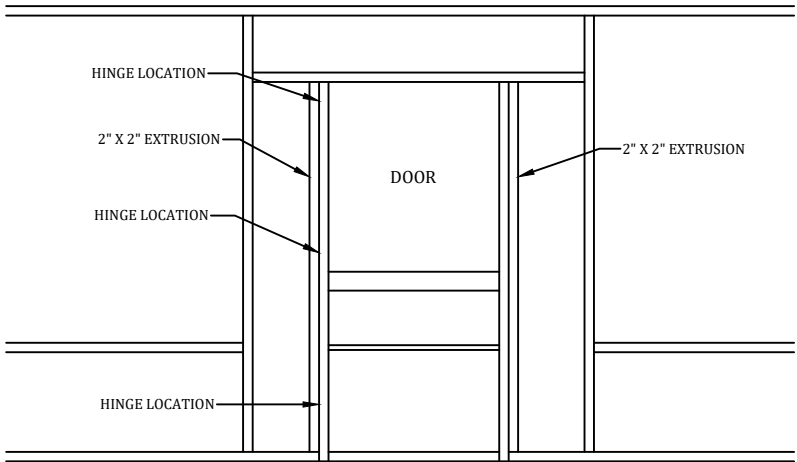

- NOTES:
1. HINGES SHALL BE ATTACHED TO STRUCTURE W/ (3) #10 X 5/8" SMS MINIMUM.
2. DOOR SHALL BE ATTACHED TO ENCLOSURE W/(2) HINGES MINIMUM.
3. HINGES SHALL BE ATTACHED TO DOOR WITH (3)#10 X 5/8" SMS. FASTEN A 1" X 2" X 0.044" TO UPRIGHT W/#12 X 1" SMS @ 12" O.C. AND WITHIN 3" FROM END OF THE UPRIGHT(IF APPLICABLE).

F

TYPICAL SCREEN DOOR CONNECTION DETAIL
SCALE: N.T.S.

PROFESSIONAL ENGINEER SEAL

P.E. OF RECORD	DAVID W. SMITH	FL 53608
	THOMAS L. HANSON	FL 38654
	IAN J. FOSTER	FL 93654
	JOEL FALARDEAU	FL 70667
	ERIK STUART	FL 77605

FBC PLANS & ENGINEERING SERVICES, INC.

ADDRESS: 5344 9th Street Zephyrhills, FL 33542

PHONE: (813)838-0735

FAX: 1-(866)824-7894

E-MAIL: erb@fbcplans.com

WEBSITE: www.fbcplans.com

C.O.A.: #29054

Florida Building Code

PLANS & ENGINEERING SERVICES, INC.

PROJECT

LANDIS 4129 HIGEL AVE SIESTA KEY, FL 34242

CONTRACTOR

REPLACE MY CAGE 6301 PORTER ROAD UNIT 12 SARASOTA, FL 34240

JOB NUMBER:

25_0902_192_LANDIS_REPLACEMC

DRAW DATE: 09/08/2025


REVISION 1:

REVISION 2:

REVISION 3:


DETAILS

S-3

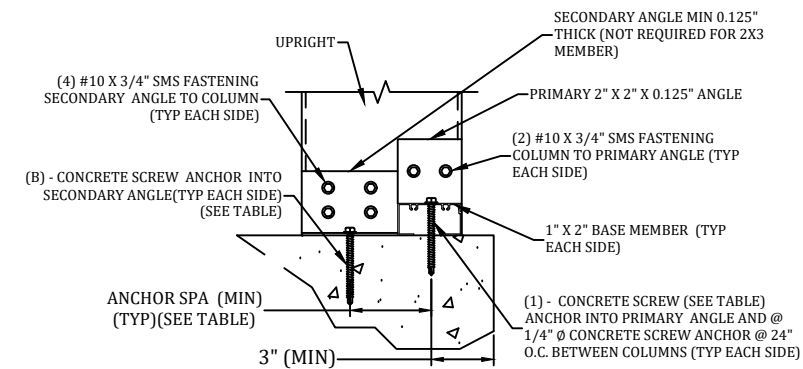


- NOTES:
1. NUMBER OF ANCHORS "B" IS EACH SIDE INTO THE SECONDARY ANGLE AND DOES NOT INCLUDE THE ANCHOR INTO THE 1X2.
 2. MINIMUM EMBEDMENT OF ANCHORS INTO CONCRETE FOOTING SHALL BE 2-3/4" AT ALL UPRIGHT LOCATIONS. ALL SCREW LENGTHS AT UPRIGHT CONNECTIONS SHALL BE OF SUFFICIENT LENGTH FOR REQUIRED EMBEDMENT INTO CONCRETE FOOTING WHEN A PAVER DECK IS PRESENT.
 3. CONCRETE SCREW ANCHOR DESIGNS ARE BASED ON THOSE LISTED ON S-1, D. FASTENERS, OTHER BRAND & TYPE SHALL BE APPROVED BY ENGINEER.
 4. 2X3W/1X2 CORNER POST SHALL REQUIRE SAME BASE CONNECTIONS AS 2X4 SHOWN IN TABLE.
 5. IF FOR AN IN-FILL, TOP OF COLUMN CONNECTION SIMILAR IF CONCRETE LINTEL.
 6. IF WOOD LINTEL/DECK, DOUBLE LEDGE REQUIRED (MIN. 3 5/8") MAY SUBSTITUTE LAG SCREW FOR LDT FOR BOTH PRIMARY & SECONDARY ANGLES.
 7. 2X2X.045 DOOR JAMB MEMBER SHALL CONNECT SIMILAR TO 2X3 MEMBER.


G 2" X 3" OR LARGER UPRIGHT TO CONCRETE W/WO PAVER
DETAILS
SCALE: N.T.S.

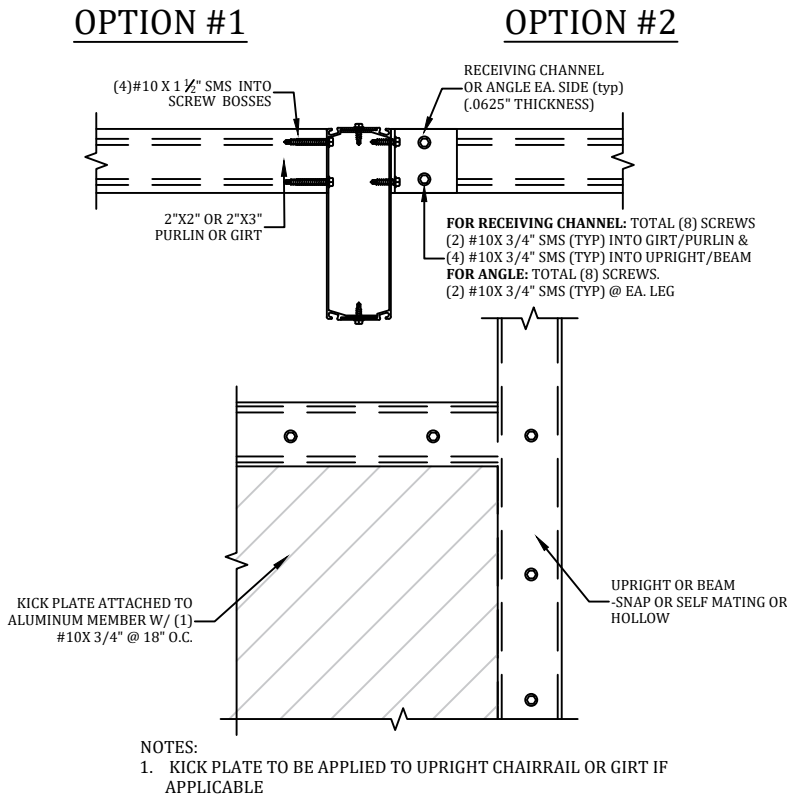


H PURLIN OR GIRT TO BEAM OR POST DETAIL
SCALE: N.T.S.

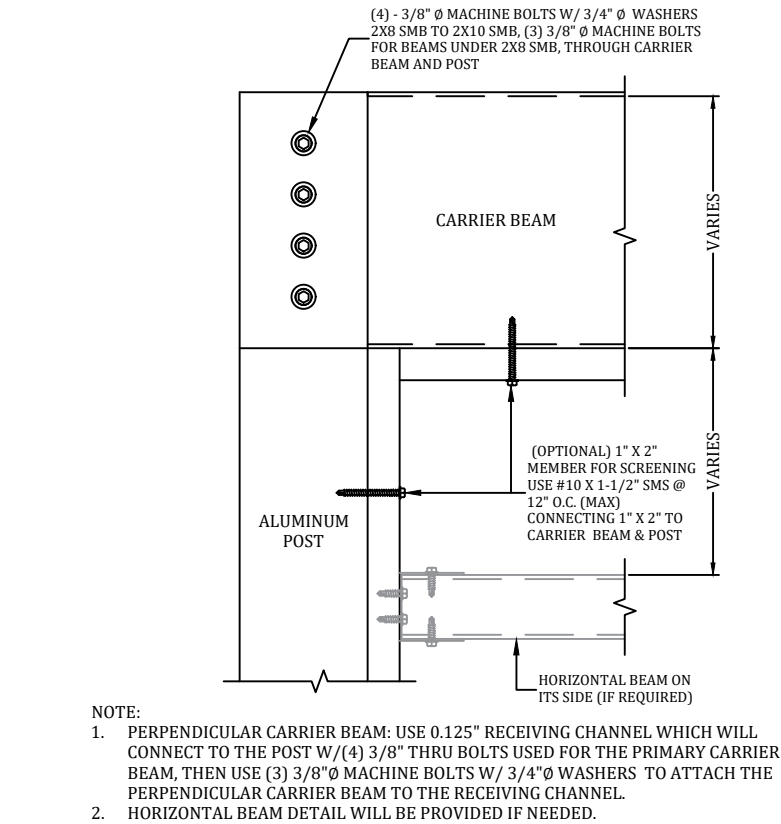

D1 BEAM TO POST DETAIL
SCALE: N.T.S.

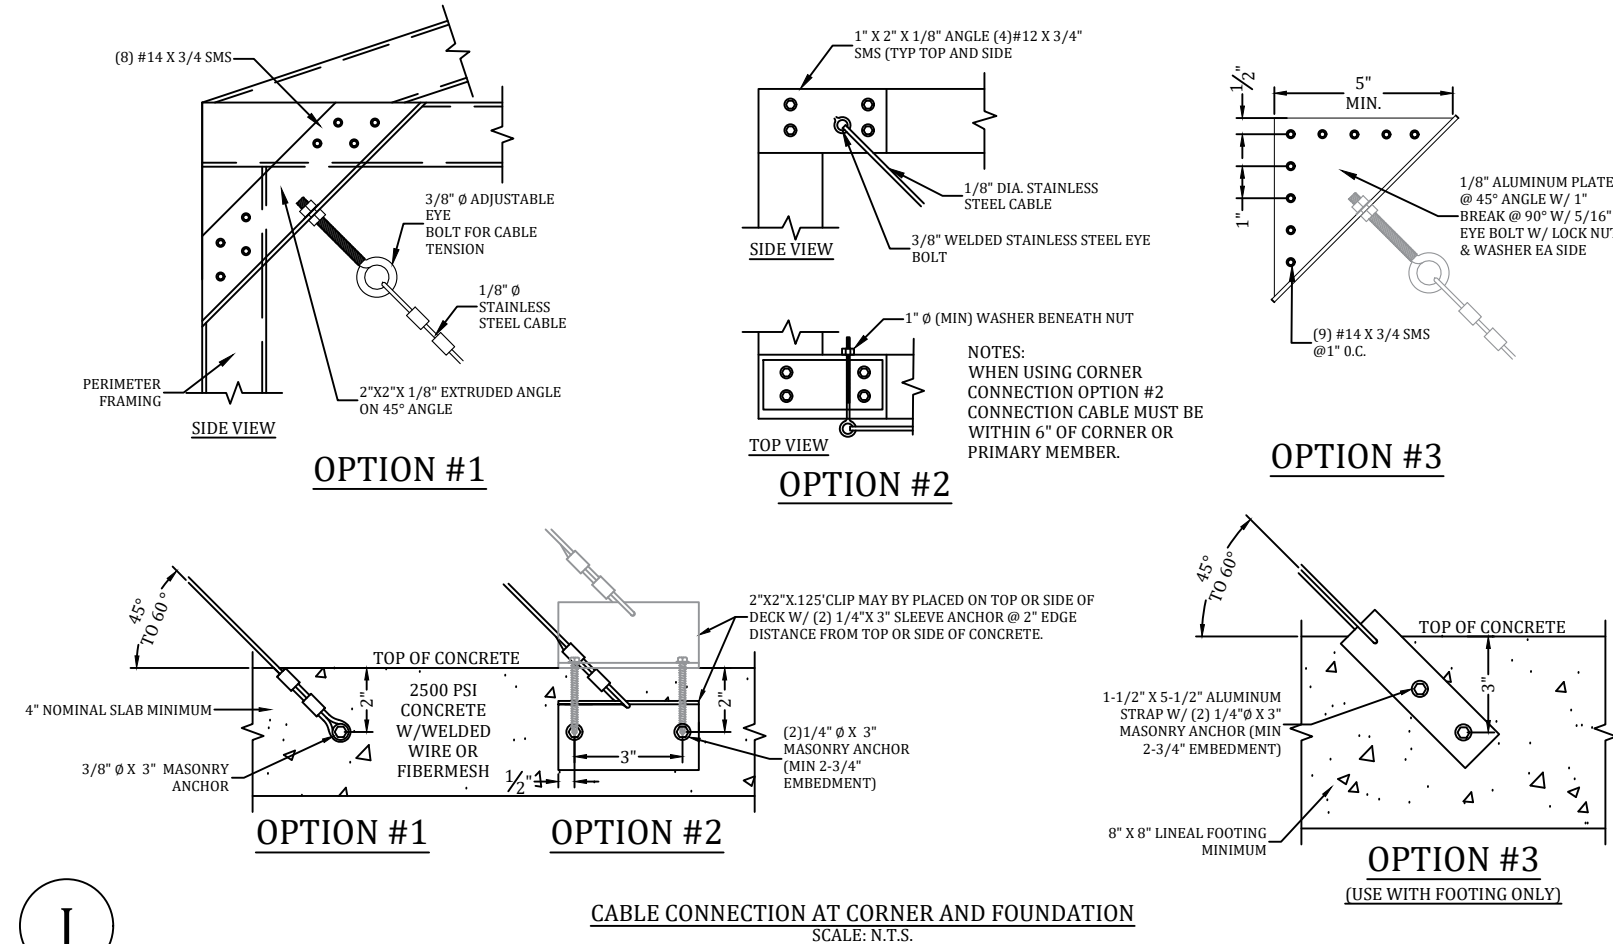

J CABLE CONNECTION AT CORNER AND FOUNDATION
SCALE: N.T.S.

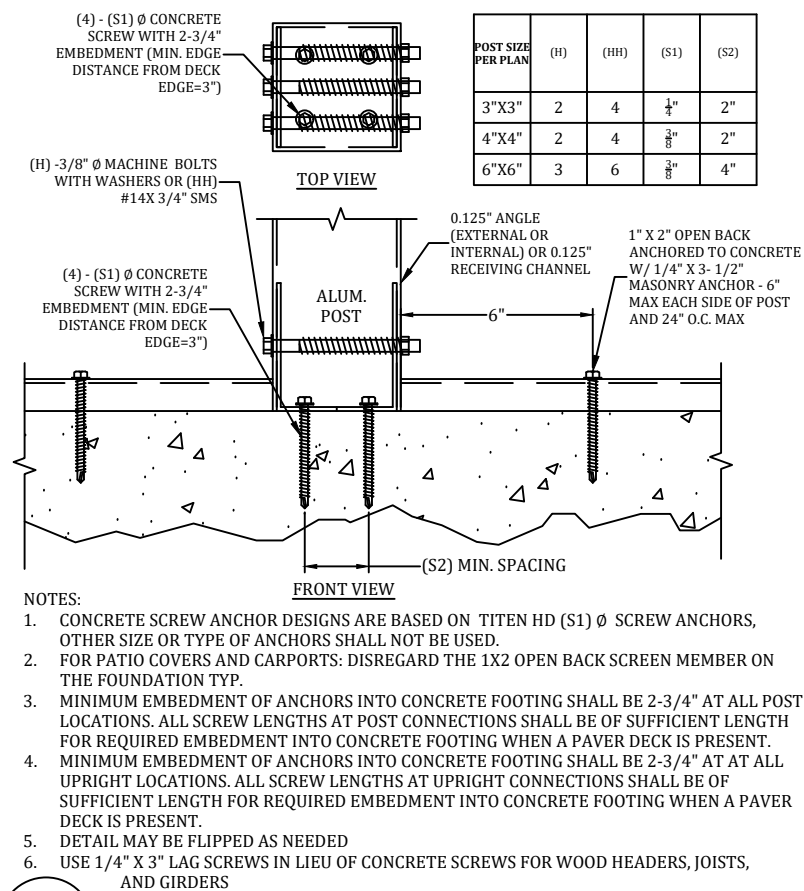

G1 ALUM. POST CONNECTION DETAIL
SCALE: N.T.S.

P.E. OF RECORD		PROFESSIONAL ENGINEER SEAL	
DAVID W. SMITH	FL 53608	THOMAS L. HANSON	FL 38654
IAN J. FOSTER	FL 93654	JOEL FALARDEAU	FL 70667
ERIK STUART	FL 77605		




FBC PLANS & ENGINEERING SERVICES, INC.	ADDRESS: 5344 9th Street Zephyrhills, FL 33542	
	PHONE: (813)838-0735	FAX: 1-(866)824-7894
Florida Building Code PLANS & ENGINEERING SERVICES, INC.	E-MAIL: erb@fbcplans.com	
	WEBSITE: www.fbcplans.com	
C.O.A.: #29054		

PROJECT	CONTRACTOR
LANDIS	REPLACE MY CAGE
4129 HIGEL AVE	6301 PORTER ROAD
SIESTA KEY, FL 34242	SARASOTA, FL 34240

JOB NUMBER:	REVISION 1:	REVISION 2:	REVISION 3:
25_0902_192_LANDIS REPLACEMENT			

DRAW DATE: 09/08/2025

DETAILS
S-4

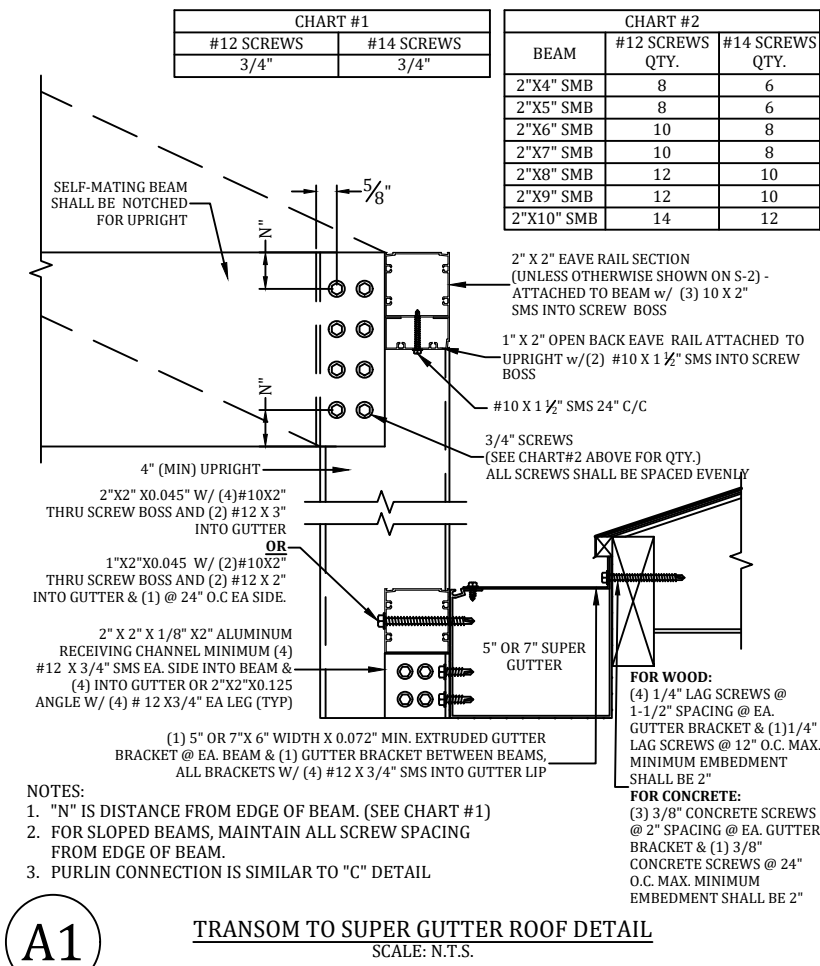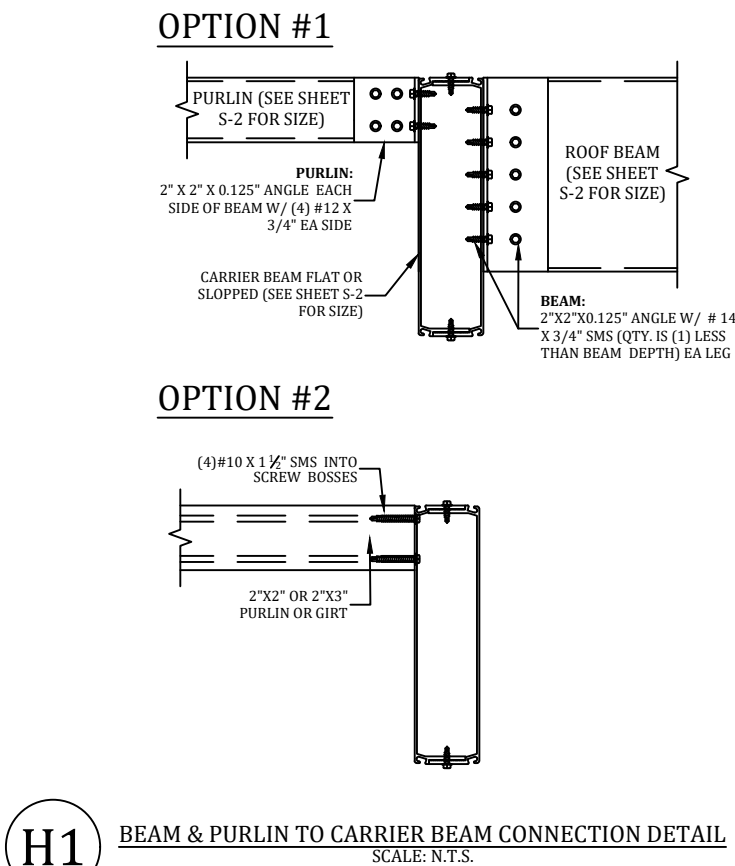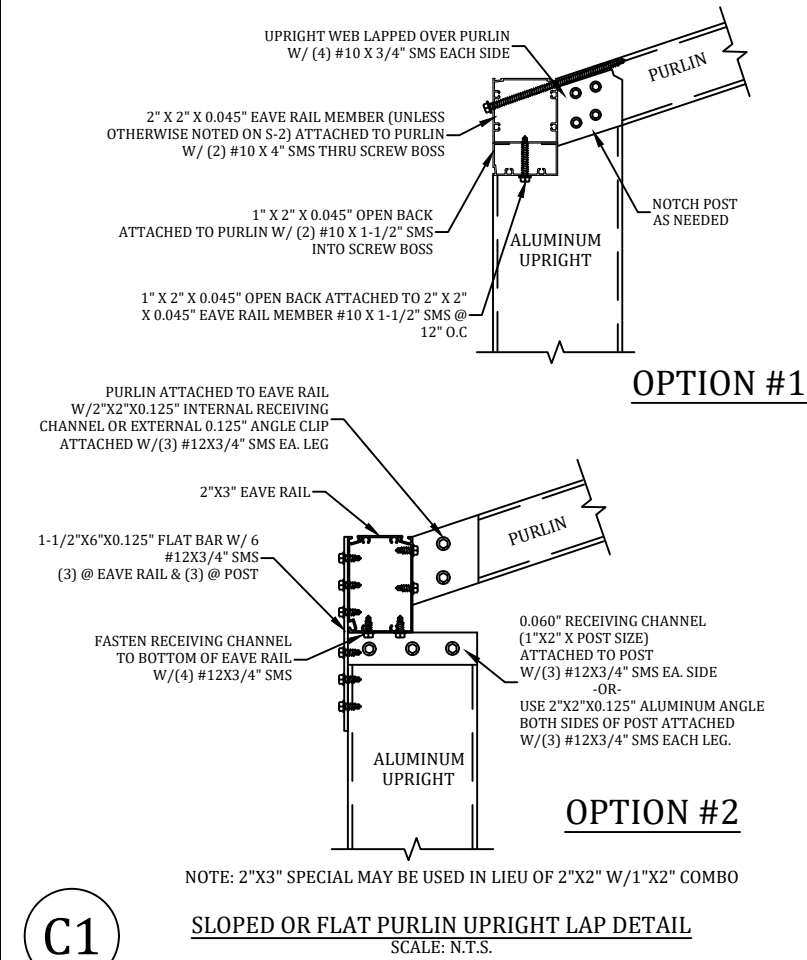

P.E. OF RECORD	DAVID W. SMITH	FL 53608
	THOMAS L. HANSON	FL 38654
FBC PLANS & ENGINEERING SERVICES, INC.	IAN J. FOSTER	FL 93654
	JOEL FALARDEAU	FL 70667
PROFESSIONAL ENGINEER SEAL	ERIK STUART	FL 77605

ADDRESS: 5344 9th Street
Zephyrhills, FL 33542

PHONE: (813)838-0735

FAX: 1-(866)824-7894

E-MAIL: erb@fbcplans.com

WEBSITE: www.fbcplans.com

C.O.A.: #29054

Florida Building Code

PLANS & ENGINEERING SERVICES, INC.

PROJECT LANDIS 4129 HIGEL AVE SIESTA KEY, FL 34242	CONTRACTOR REPLACE MY CAGE 6301 PORTER ROAD UNIT 12 SARASOTA, FL 34240			
JOB NUMBER: 25_0902_192_LANDIS REPLACEMENT	DRAW DATE: 09/08/2025	REVISION 1:	REVISION 2:	REVISION 3:
DETAILS				
S-5				