

GENERAL NOTES SECTIONS

A. CONCRETE & FOUNDATION DESIGN:

- ALL CONCRETE AND FOUNDATIONS ATTACHED TO THE HOST STRUCTURE SHALL HAVE A PRE INSPECTION.
- SOIL BEARING PRESSURE SHALL BE A MINIMUM OF 1500 PSF. THE BEARING CAPACITY OF THE SOIL TO BE VERIFIED BY A LICENSED CONTRACTOR PRIOR TO ANY POURING OF CONCRETE.
- ALL CONCRETE GRADE BEAMS AND FOOTINGS SHALL BE 3000 PSI MINIMUM.
- ALL SLABS ON GRADE SHALL BE A MINIMUM OF 4"THICK WITH FIBERMESH OR WIREMESH REINFORCING.
- ALL OVER POUR CONCRETE FILLED SUPPORTED SLABS SHALL BE 3000 PSI MIN., 2" MIN. THICKNESS WITH EPOXY.
- THE CONCRETE SHALL CONFORM TO ASTM C94 FOR THE FOLLOWING:
 - OPC (PORTLAND CEMENT TYPE 1,- ASTM C 150).
 - AGGREGATES - #6 STONE , ASTM C 33 SIZE NO. 67 LESS THAN 3/4".
 - AIR ENTRAINING +/- 1% - ASTM C 260.
 - WATER REDUCING AGENT - ASTM C 494.
 - CLEAN POTABLE WATER.
 - OTHER ADMIXTURES SHALL NOT BE PERMITTED.
- FIBERMESH REINFORCEMENT TO BE 3000 PSI (3/4" PER CUBIC YARD MIN.) AND MEET APPROPRIATE ACI AND ASTM REQUIREMENTS.
- METAL BARS SHALL CONFORM TO ASTM A 185.
- ALL REINFORCING SHALL CONFORM TO ASTM A615,BE GRADE 60 (60 KSI MIN.) DEFORMED BARS, #3 BARS MAY BE GRADE 40.
- PREPARE & PLACE CONCRETE ACCORDING TO AMERICAN CONCRETE INSTITUTE MANUAL STANDARD PRACTICE, PART 1, 2, & 3 ALONG WITH HOT WEATHER CONDITIONS RECOMMENDATIONS.
- IF UTILIZING EXISTING CONCRETE FOR FOUNDATION, CONCRETE SHALL BE A MINIMUM OF 4" IN THICKNESS, VISIBLY FREE OF ANY STRUCTURAL EXCESSIVE CRACKING, SPALLING OR OTHER DETERIORATION.
- CONTRACTOR TO FIELD VERIFY ANY EXISTING FOUNDATIONS NOTED ON SHEET S-1, DESIGN DATA: NOTE 10.
- DRY PACKING/POURING** IS NOT PERMITTED

B. MASONRY:

- CONCRETE MASONRY UNITS (CMU) SHALL BE STANDARD HOLLOW UNITS AND SHALL BE 2000 PSI MINIMUM BASED ON TYPE M OR S MORTAR.
- ALL MORTAR SHALL BE OF TYPE M OR S.
- ALL GROUT SHALL BE 2000 PSI MINIMUM AND HAVE MAXIMUM COARSE AGGREGATE SIZE OF 3/8".
- PROVIDE CLEAN-OUTS FOR REINFORCED CELLS CONTAINING REINFORCEMENT WHEN GROUT POUR EXCEEDS 5'-0" IN HEIGHT.

C. ALUMINUM:

- ALL STRUCTURAL ALUMINUM SHALL CONFORM TO THE MINIMUM REQUIREMENTS OF 6005-T5 FOR ALLOY WITH A MINIMUM THICKNESS OF 0.040" FOR SUPPORTING MEMBERS.
- ALL PLATES, ANGLES, AND CHANNELS SHALL BE 6005 T5 OR T6 ALLOY.
- WHERE KICK PLATES ARE USED A MINIMUM THICKNESS OF 0.024" SHALL APPLY.
- STRUCTURAL ALUMINUM DESIGN CONFORMS TO "PART 1-A - SPECIFICATIONS FOR ALUMINUM STRUCTURES - ALLOWABLE STRESS DESIGN" OR "PART 1-B - SPECIFICATIONS FOR ALUMINUM STRUCTURES - BUILDING LOAD AND RESISTANCE FACTOR DESIGN" OF THE ALUMINUM DESIGN MANUAL PREPARED BY THE ALUMINUM ASSOCIATION, INC.WASHINGTON D.C. FLORIDA BUILDING CODE EIGHTH EDITION (2023), BUILDING (CHAPTER 16 STRUCTURAL DESIGN & CHAPTER 20 ALUMINUM).
- WHERE ALUMINUM COMES INTO CONTACT WITH STEEL, OR PRESSURE TREATED LUMBER PROVIDE DIELECTRIC SEPARATION.
- ALUMINUM SELF MATING BEAM MEMBERS SHALL BE STITCHED WITH NO LESS THAN #10 SMS 6" FROM THE ENDS AND 12" ON CENTER, IF USING #12 SPACING MAY BE 24" ON CENTER.
- VINYL AND ACRYLIC PANELS SHALL BE REMOVABLE. THEY SHALL BE IDENTIFIED WITH A DECAL ESSENTIALLY STATING "REMOVABLE PANEL SHALL BE REMOVED WHEN WIND SPEEDS EXCEED 75 MPH" .

- DECAL SHALL BE PLACED SO IT IS VISIBLE WHEN PANEL IS INSTALLED. VINYL AND ACRYLIC PANELS MAY NOT BE USED IN FLOOD ZONE A.
- 1"x2"x0.040" NON-STRUCTURAL MEMBERS SHALL BE ATTACHED TO HOST WITH 1/4"Ø X 1-3/4" EMBEDMENT & 24" O.C. MASONRY SCREW FOR CONCRETE & EQUIVALENT SIZE WOOD SCREW WHEN IN WOOD & #10X 1/2" EMBEDMENT SMS OR TEK SCREWS IN ALUMINUM MEMBERS TYPICAL.
 - ALL 5",7", AND 9" GUTTERS SHALL BE STRUCTURAL GUTTERS

D. FASTENERS:

- ALL LAG BOLTS SHALL CONFORM TO STAINLESS STEEL TYPE 300 18-8, WITH STANDARD FLAT WASHER UNLESS MANUFACTURER GALVANIZES BOLTS SPECIFIES FOR USE WITH ACQ PRESSURE TREATED WOOD.
- HEX BOLTS HAS TO BE ASTM A 325, PLATED WITH STANDARD FLAT WASHERS AND NUTS.
- ALL CONCRETE SCREWS SHALL BE, SIMPSON, HILTI, RAWL, TAPCON, REDHEAD, DYNABOLT, PORTECT OR APPROVED EQUAL.
- ALL METAL TIES AND ASSOCIATED ACCESSORIES SHALL BE HOT DIPPED GALVANIZED.
- ALL LAG BOLTS SHALL HAVE A MINIMUM EMBEDMENT OF 8X BOLT DIAMETER INTO STRUCTURAL FRAMING (G=42 MIN.).
- LAG BOLTS AND SCREWS INTO WOOD FRAMING SHALL BE PROVIDED WITH PILOT HOLES HAVING A DIAMETER NOT GREATER THAN 70 PERCENT OF THE THREAD DIAMETER OF THE BOLT OR SCREW. ALL LAG BOLTS AND SCREWS SHALL BE INSERTED IN PILOT HOLES BY TURNING AND UNDER NO CIRCUMSTANCES BY DRIVING WITH A HAMMER.
- ALL EXPANSION ANCHORS SHALL BE DESIGNED IN ACCORDANCE WITH THE SPECIFIC MANUFACTURER'S REQUIREMENTS AND ALLOWABLE LOADS AND SHALL ONLY BE APPLIED IN CONDITIONS ACCEPTABLE TO MANUFACTURER. FASTENERS SHALL BE A MINIMUM OF SAE GRADE #5 OR BETTER ZINC PLATED.
- ALL FASTENERS CONNECTING ALUMINUM COMPONENTS OR PRESSURE TREATED LUMBER ARE STAINLESS STEEL TYPE 300 18-8, UNLESS MANUFACTURER GALVANIZED BOLTS SPECIFIES FOR USE WITH ACQ PRESSURE TREATED WOOD, OR OTHERWISE NOTED ON PLANS.
- ALL FASTENERS SHALL COMPLY WITH ASTM A153.
- ALL CONNECTORS SHALL COMPLY WITH ASTM A653 CLASS G-185.
- FOR SMS, THE MINIMUM CENTER-TO-CENTER SPACING SHALL BE 3/4" AND MINIMUM CENTER-TO-EDGE SHALL BE 1/2" UNLESS NOTED OTHER WISE.

E. REFERENCE STANDARDS: (CURRENT EDITIONS OF)

ASTM E 119
ASTM E 1300
ASCE 7
ALUMINUM DESIGN MANUAL-AA ASM35, AND SPEC. FOR ALUMINUM PART 1-A, & 1-B
ASTM C94
ASTM C150
ASTM C33
ASTM C260
ASTM C494
ASTM A615
ASTM A185
FLORIDA BUILDING CODE EIGHTH EDITION (2023), BUILDING
FLORIDA BUILDING CODE EIGHTH EDITION (2023), RESIDENTIAL
FLORIDA BUILDING CODE EIGHTH EDITION (2023), EXISTING
HUD CODE

F. ABBREVIATIONS:

- THE FOLLOWING LIST OF ABBREVIATIONS IS NOT INTENDED TO REPRESENT ALL THOSE USED ON THESE DRAWINGS, BUT TO SUPPLEMENT THE MORE COMMON ABBREVIATIONS.
- TYP -- TYPICAL
 - SIM -- SIMILAR
 - UON -- UNLESS OTHERWISE NOTED
 - CONT -- CONTINUOUS
 - VIF -- VERIFY IN FIELD
 - SMB -- SELF MATING BEAM
 - FSM -- FLORIDA SALES AND MARKETING
 - REC -- RECEIVING CHANNEL

G. RESPONSIBILITY:

- ALL SITE WORK SHALL BE PERFORMED BY A LICENSED CONTRACTOR IN ACCORDANCE WITH APPLICABLE BUILDING CODES, LOCAL ORDINANCES, ETC.
- CONTRACTOR SHALL VERIFY ALL DIMENSIONS AND DETAILS, NOTIFYING ENGINEER OF ANY DISCREPANCIES BETWEEN DRAWINGS, FABRICATED ITEMS, OR ACTUAL FIELD CONDITIONS.
- ALL DETAILS ON THESE DRAWINGS ARE ENGINEERED BASED ON INFORMATION PROVIDED BY THE CONTRACTOR AND/OR MANUFACTURER.
- ANY DETAILS NOT SHOWN ARE TO BE ENGINEERED BY A LICENSED P.E. IN ACCORDANCE WITH STANDARD ENGINEERING PRACTICES.
- WHEN ATTACHING TO FASCIA, THE HOST STRUCTURE SHALL HAVE AT LEAST A 2"x4" FASCIA AND ROOF TRUSS SYSTEM. CONTRACTOR SHALL VERIFY THIS AND IF SMALLER, CONTRACTOR SHALL BRING STRUCTURE UP TO A 2"x4" FASCIA AND ENSURE LESS THAN A 2'-0" OVERHANG.
- FBC PLANS & ENGINEERING SERVICES INC. DOES NOT WARRANT, EITHER EXPRESSLY OR IMPLIED, THE QUALITY OF THE CONSTRUCTION, AND IS NOT RESPONSIBLE FOR THE INTERPRETATION OF DESIGNS AND END USE BY THE CLIENT/CONTRACTOR.
- CONTRACTOR TO VERIFY FEMA FLOOD ZONE OF THE PROPOSED STRUCTURE LOCATION TO ENSURE STRUCTURE IS NOT WITHIN SPECIAL FLOOD HAZARD AREAS.
- MISCELLANEOUS:**
 - ALUMINUM ADDITIONS ARE NOT TO BE INSTALLED ON A MANUFACTURED HOME, TRAILER HOME, OR PRE-FAB HOME. IF NO HOST BEAM IS PRESENT, A SEPARATE 4TH WALL SUPPORT SYSTEM MUST BE ENGINEERED TO ENSURE NO ADDITIONAL LOADING IS PLACED ON THE MANUFACTURED HOME.
 - IF ENCLOSURE CONTAINS A SWIMMING POOL OR SPA, THE ENCLOSURE SHALL COMPLY WITH RESIDENTIAL SWIMMING BARRIER REQUIREMENTS OF FLORIDA BUILDING CODE EIGHTH EDITION (2023), RESIDENTIAL R 4501.17 IN ITS ENTIRETY.
 - DOOR LOCATIONS MAY BE DETERMINED IN THE FIELD BY CONTRACTOR.
 - IF PAVERS ARE UNDER ALUMINUM MEMBERS THEY SHALL HAVE EPOXY ADHESIVE TO CONCRETE OR IF USING GROUT, ENSURE BONDING AGENT IS USED FIRST AND ADHERED WITH MINIMUM 3000 PSI GROUT.
 - SCREENING MATERIAL SHALL BE 18X14X0.013 OR EQUIVALENT DENSITY SCREEN MESH ONLY UNLESS NOTED ON DRAWING S-2.
 - ALL STRUCTURAL POST SHALL BE ANCHORED TO AN EXISTING/PROPOSED CONCRETE FOUNDATION FOR UPLIFT PURPOSES.
 - CONTRACTOR TO ENSURE ALL PROPOSED GUTTERS HAVE A POSITIVE FLOW.
 - EMERGENCY ESCAPE & RESCUE OPENING PER FBC R310.1 SHALL BE VERIFIED BY CONTRACTOR & BUILDING OFFICIAL.
 - ENCLOSED ADDITIONS TO MANUFACTURED HOMES SHALL NOT CHANGE THE EXIT FACILITIES FOR EGRESS PER HUD 3280.105, (A) THROUGH (A)(2)(IV), SO THAT THE DISTANCE TO EXIT DIRECTLY OUTSIDE FROM ALL BEDROOMS IS LESS THAN 35', AND, SO THAT TWO EXITS DIRECTLY OUTSIDE ARE STILL MAINTAINED. A CARPORT OR SCREEN ROOM SHALL BE CONSIDERED AS OUTSIDE. NON-HABITABLE SUNROOMS OR HABITABLE LIVING SPACE MAY BE ADDED WHERE AN EXIT DOOR WAS LOCATED AS LONG AS A NEW EXIT DOOR IS ADDED AND MEETS THE REQUIREMENTS OF HUD 3280.105.
 - AWS CERTIFIED WELDER REQUIRED FOR ALL WELDING.

SCREEN ENCLOSURE

DESIGN DATA: (SITE SPECIFIC DESIGN INFORMATION)

- ULTIMATE DESIGN WIND SPEED Vult, (3 SECOND GUST): 135 MPH
- NOMINAL DESIGN WIND SPEED Vasd: 105 MPH
- RISK CATEGORY: 1
- WIND EXPOSURE: C
- WIND LOADS:

SCREEN ROOF: 10 PSF

SCREEN WALLS (WINDWARD): 35 PSF

SCREEN WALLS (LEEWARD): 28 PSF

SOLID ROOF: N/A
- FACTOR APPLIED TO SCREEN WIND LOADS FOR 18/14: 0.88
- FACTOR APPLIED TO SCREEN WIND LOADS FOR 20/20: 1.0
- MESH TYPE AND LOCATION SHOWN ON S-2
- FACTORS FOR OTHER SCREEN MESHES TO BE DETERMINED BY THE ENGINEER
- FACTOR APPLIED TO SCREEN WIND LOADS FOR ALLOWABLE STRESS DESIGN: 0.6
- LIVE LOAD: 0.6
- 300 lb. VERTICAL DOWNLOAD ON PRIMARY SCREEN ENCLOSURE MEMBERS.
- 200 lb. VERTICAL DOWNLOAD ON SCREEN ENCLOSURE PURLINS.
- SCREEN ROOF TYPE: MANSARD
- NON-SCREEN ROOF TYPE: N/A
- EXISTING FOOTING (MIN. 12"x 12" LINEAL FOOTING) MEETS THE REQUIREMENTS TO RESIST THE UPLOADS FOR THE PROPOSED STRUCTURE.

ALUMINUM STRUCTURAL MEMBERS

HOLLOW SECTIONS

2 X 2:-----2" X 2" X 0.044"
2 X 3:-----2" X 3" X 0.050"
2 X 4:-----2" X 4" X 0.050"
2 X 5:-----2" X 5" X 0.050"
3 X 3:-----3" X 3" X 0.125"

OPEN BACK SECTIONS

1 X 2:-----1" X 2" X 0.040"
1 X 3:-----1" X 3" X 0.045"

SNAP SECTIONS

2 X 2 SMS:-----2" X 2" X 0.045"
2 X 3 SMS:-----2" X 3" X 0.072"
2 X 4 SMS:-----2" X 4" X 0.045"
3 X 3 SMS:-----3" X 3" X 0.090"

SELF MATING (SMB)

2 X 4 SMB:-----2" X 4" X 0.044" X 0.100"
2 X 5 SMB:-----2" X 5" X 0.050" X 0.118"
2 X 6 SMB:-----2" X 6" X 0.050" X 0.120"
2 X 7 SMB:-----2" X 7" X 0.057" X 0.120"
2 X 8 SMB:-----2" X 8" X 0.072" X 0.224"
2 X 9 SMB:-----2" X 9" X 0.072" X 0.224"
2 X 10 SMB:-----2" X 10" X 0.092" X 0.374"

TUBE SECTIONS

2 X 2:-----2" X 2" X 0.090"

INDEX

S-1

S-2

S-3

S-4


NOTES
DRAWING
DETAILS
DETAILS

BB T

PROFESSIONAL ENGINEER SEAL														
JOB NUMBER: 26_0224_840_HUDDLESTON_REPLACEMENTC			PROJECT HUDDLESTON 7321 CAYMAN CT PALMETTO, FL 34221			Florida Building Code PLANS & ENGINEERING SERVICES, INC				FBC PLANS & ENGINEERING SERVICES, INC.			P.E. OF RECORD	
DRAW DATE: 02/24/2026						ADDRESS: 5344 9th Street Zephyrhills, FL 33542				DAVID W. SMITH		FL 53608		
REVISION 1:						PHONE: (813)838-0735				THOMAS L. HANSON		FL 38654		
REVISION 2:						FAX: 1-(866)824-7894				IAN J. FOSTER		FL 93654		
REVISION 3:						E-MAIL: erb@fbcplans.com				JOEL FALARDEAU		FL 70667		
						WEBSITE: www.fbcplans.com				ERIK STUART		FL 77605		
						C.O.A.: #29054								
NOTES														
S-1														


A

GUTTER BRACKET & BEAM ATTACHMENT DETAIL
SCALE: N.T.S.

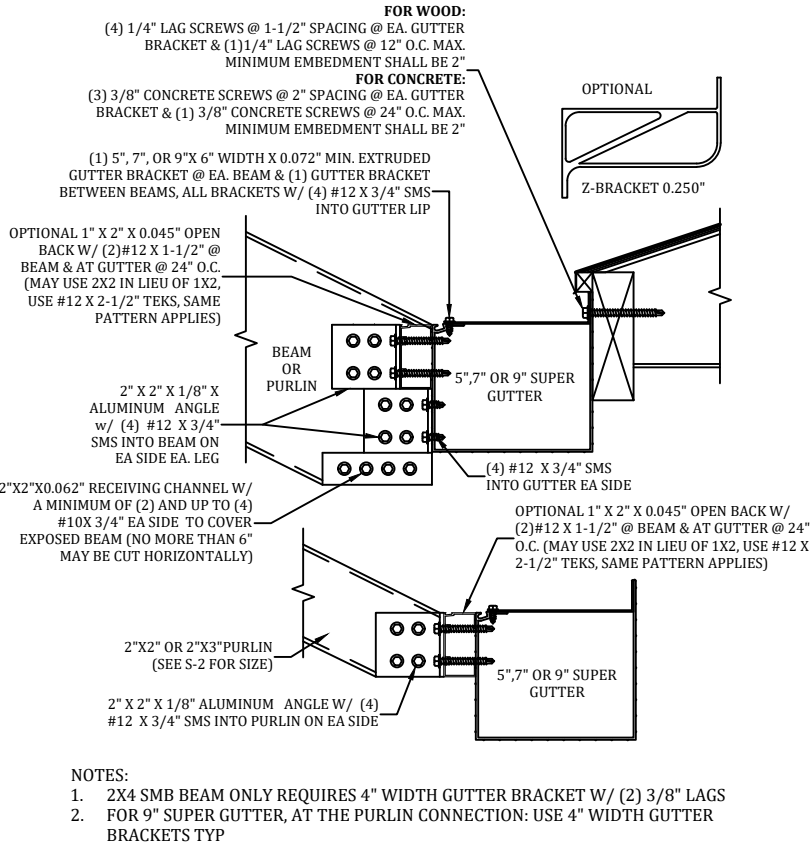


B

BEAM SPLICE GUSSET DETAIL
SCALE: N.T.S.

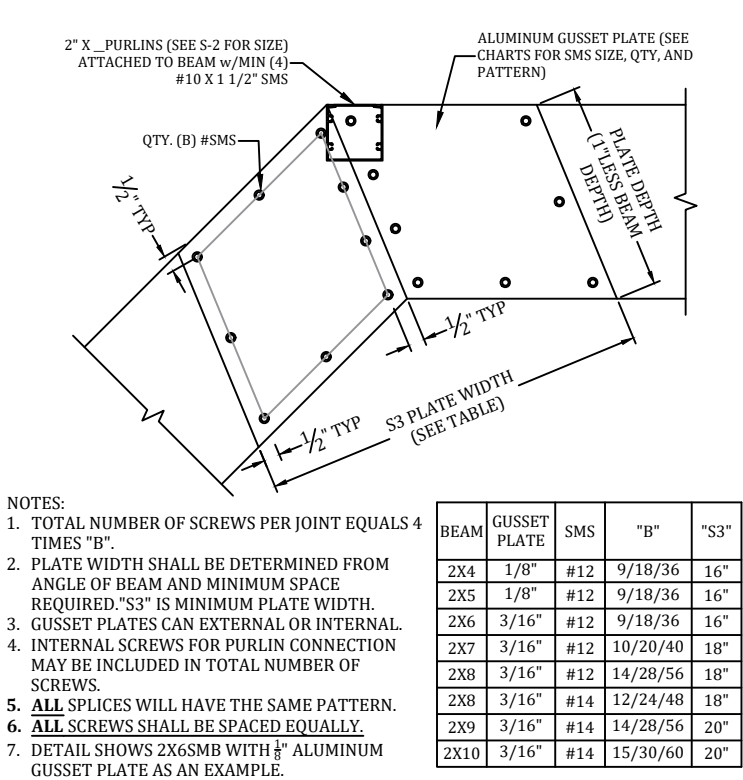


C

SLOPED OR FLAT PURLIN CONNECTION DETAIL
SCALE: N.T.S.

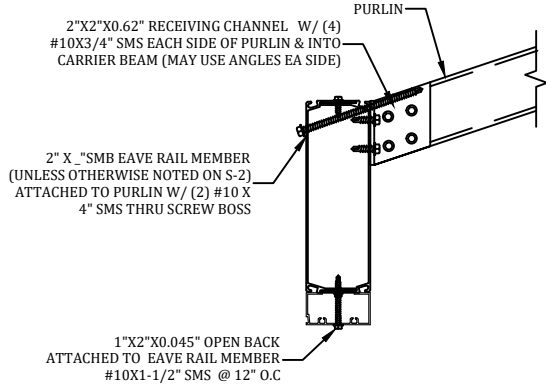


D

BEAM TO CARRIER BEAM CONNECTION DETAIL
SCALE: N.T.S.

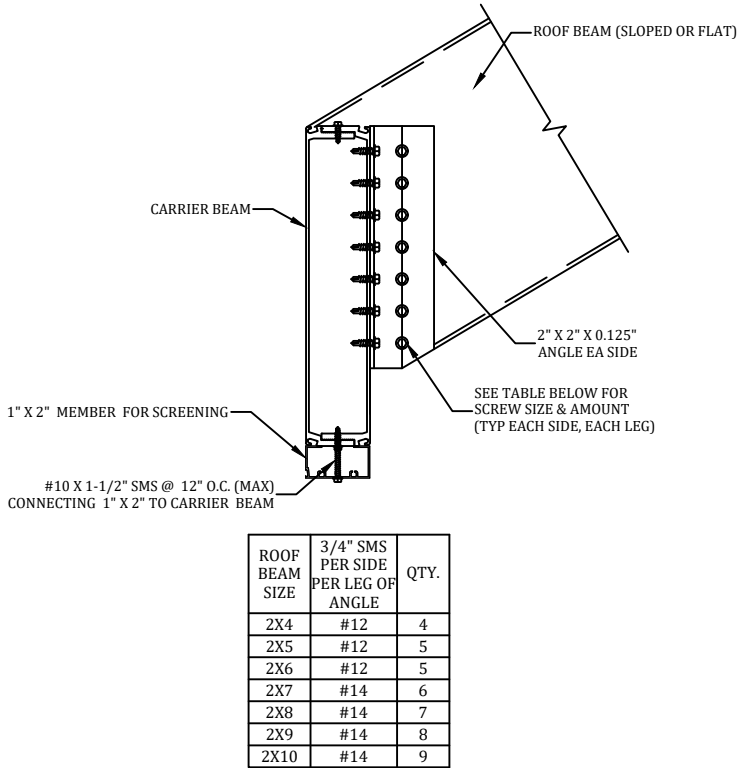


E

ROOF BRACING CONNECTION DETAIL
SCALE: N.T.S.

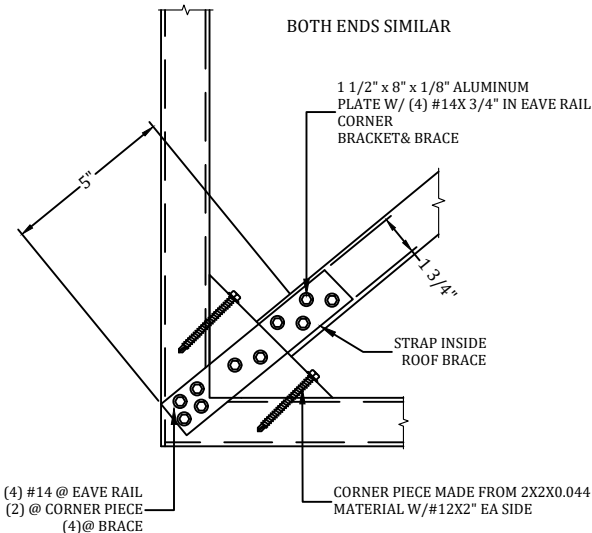

F

TYPICAL SCREEN DOOR CONNECTION DETAIL
SCALE: N.T.S.

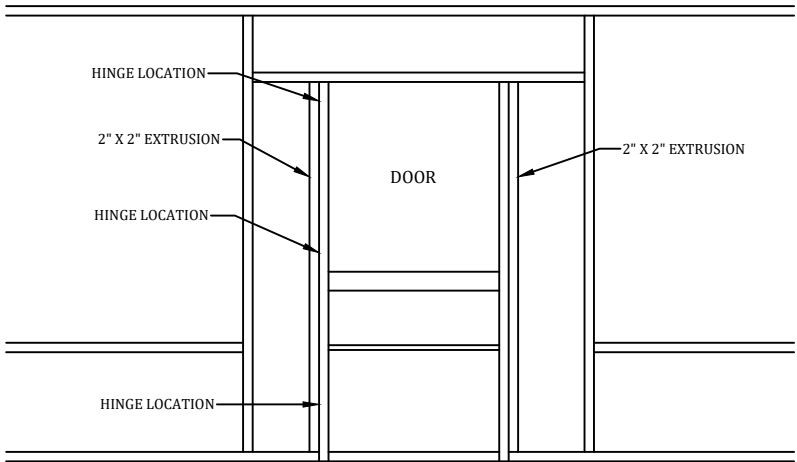

- NOTES:
1. HINGES SHALL BE ATTACHED TO STRUCTURE W/ (3) #10 X 5/8" SMS MINIMUM.
2. DOOR SHALL BE ATTACHED TO ENCLOSURE W/(2) HINGES MINIMUM.
3. HINGES SHALL BE ATTACHED TO DOOR WITH (3)#10 X 5/8" SMS. FASTEN A 1" X 2" X 0.044" TO UPRIGHT W/#12 X 1" SMS @ 12" O.C. AND WITHIN 3" FROM END OF THE UPRIGHT(IF APPLICABLE).


P.E. OF RECORD		PROFESSIONAL ENGINEER SEAL	
DAVID W. SMITH	FL 53608	THOMAS L. HANSON	FL 38654
IAN J. FOSTER	FL 93654	JOEL FALARDEAU	FL 70667
ERIK STUART	FL 77605		

FBC PLANS & ENGINEERING SERVICES, INC.	ADDRESS: 5344 9th Street Zephyrhills, FL 33542	
	PHONE: (813)838-0735	FAX: 1-(866)824-7894
Florida Building Code PLANS & ENGINEERING SERVICES, INC.	E-MAIL: erb@fbcplans.com	
	WEBSITE: www.fbcplans.com	
C.O.A.: #29054		

PROJECT	CONTRACTOR
HUDDLESTON	REPLACE MY CAGE
7321 CAYMAN CT	6301 PORTER ROAD
PALMETTO, FL 34221	SARASOTA, FL 34240
UNIT 12	


JOB NUMBER:	REVISION 1:	REVISION 2:	REVISION 3:
26_0224_840_HUDDLESTON_REPLACMC			
DRAW DATE: 02/24/2026			

DETAILS	
S-3	

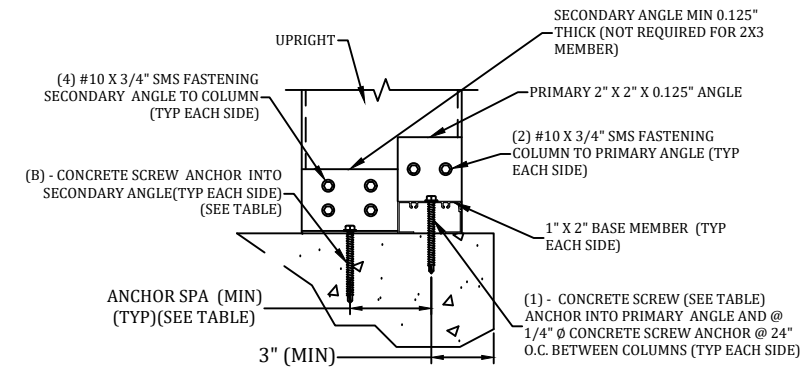


- NOTES:
1. NUMBER OF ANCHORS "B" IS EACH SIDE INTO THE SECONDARY ANGLE AND DOES NOT INCLUDE THE ANCHOR INTO THE 1X2.
 2. MINIMUM EMBEDMENT OF ANCHORS INTO CONCRETE FOOTING SHALL BE 2-3/4" AT ALL UPRIGHT LOCATIONS. ALL SCREW LENGTHS AT UPRIGHT CONNECTIONS SHALL BE OF SUFFICIENT LENGTH FOR REQUIRED EMBEDMENT INTO CONCRETE FOOTING WHEN A PAVER DECK IS PRESENT.
 3. CONCRETE SCREW ANCHOR DESIGNS ARE BASED ON THOSE LISTED ON S-1, D. FASTENERS, OTHER BRAND & TYPE SHALL BE APPROVED BY ENGINEER.
 4. 2X3W/1X2 CORNER POST SHALL REQUIRE SAME BASE CONNECTIONS AS 2X4 SHOWN IN TABLE.
 5. IF FOR AN IN-FILL, TOP OF COLUMN CONNECTION SIMILAR IF CONCRETE LINTEL.
 6. IF WOOD LINTEL/DECK, DOUBLE LEDGE REQUIRED (MIN. 3 5/8") MAY SUBSTITUTE LAG SCREW FOR LDT FOR BOTH PRIMARY & SECONDARY ANGLES.
 7. 2X2X.045 DOOR JAMB MEMBER SHALL CONNECT SIMILAR TO 2X3 MEMBER.
 8. SEE S-1, DESIGN DATA: NOTE 10 FOR FOUNDATION INFORMATION.


G 2" X 3" OR LARGER UPRIGHT TO CONCRETE W/WO PAVER
DETAILS
SCALE: N.T.S.

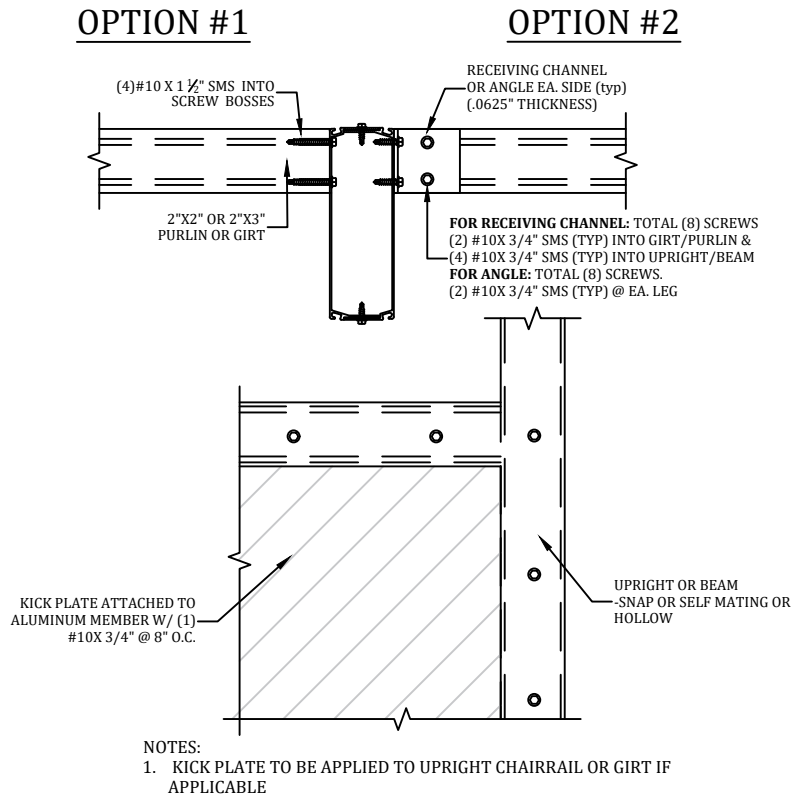


H PURLIN OR GIRT TO BEAM OR POST DETAIL
SCALE: N.T.S.

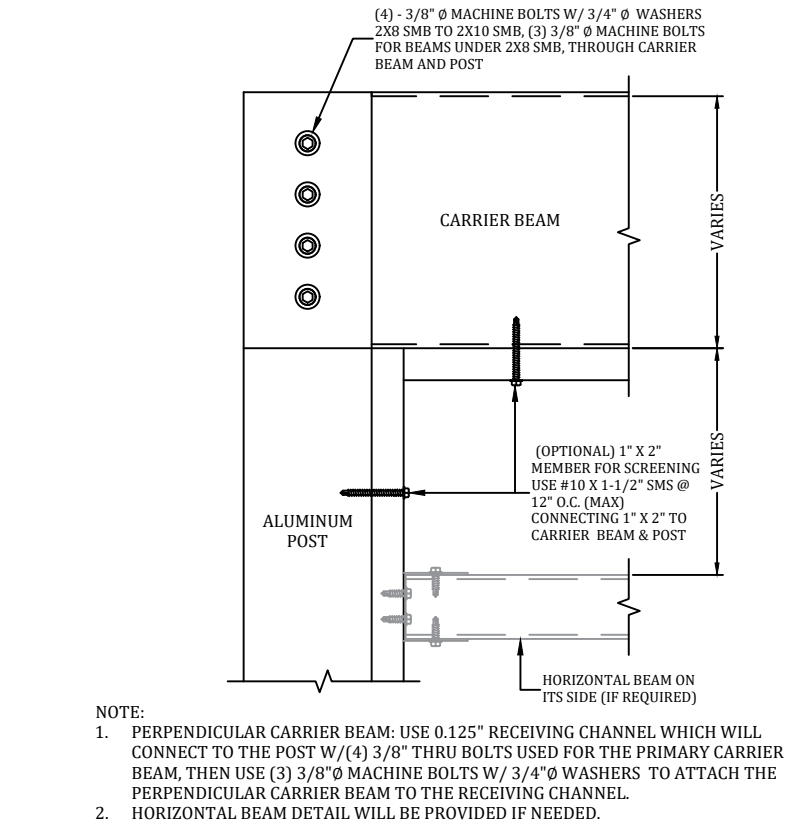

D1 BEAM TO POST DETAIL
SCALE: N.T.S.

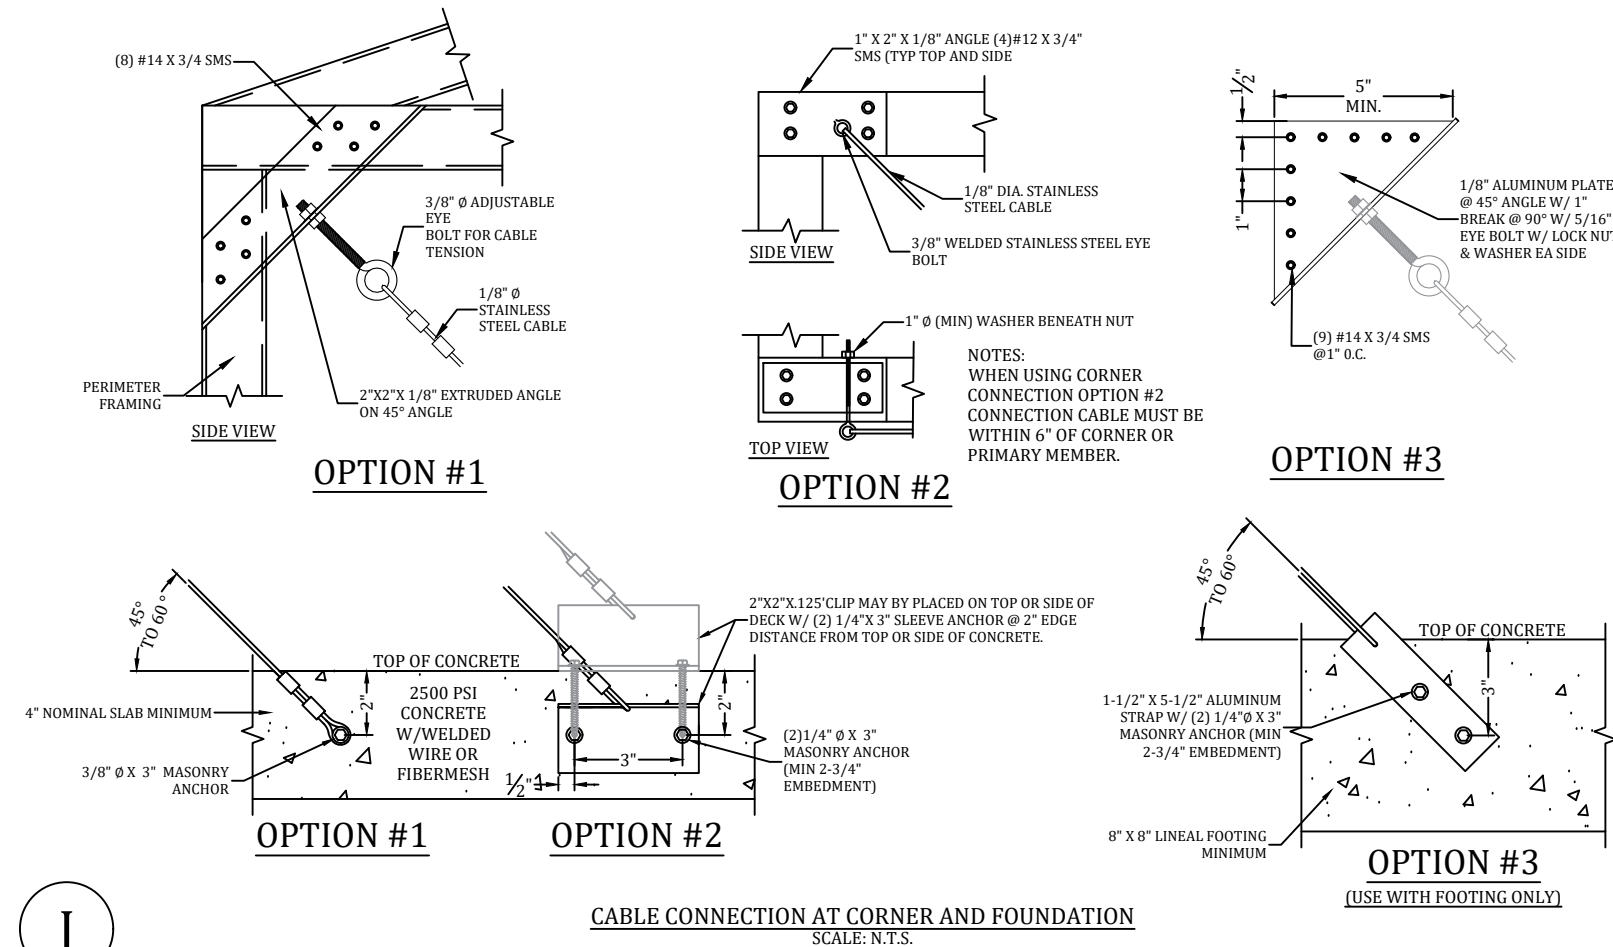

J CABLE CONNECTION AT CORNER AND FOUNDATION
SCALE: N.T.S.

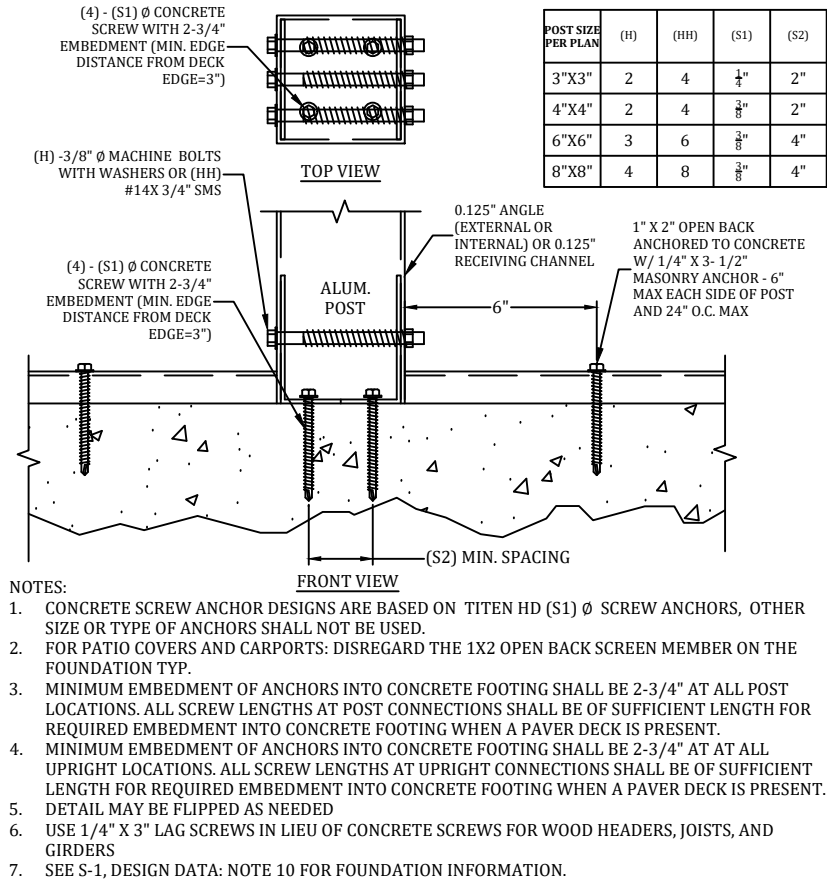

G1 ALUM. POST CONNECTION DETAIL
SCALE: N.T.S.

P.E. OF RECORD	
DAVID W. SMITH	FL 53608
THOMAS L. HANSON	FL 38654
IAN J. FOSTER	FL 93654
JOEL FALARDEAU	FL 70667
ERIK STUART	FL 77605

FBC PLANS & ENGINEERING SERVICES, INC.	
ADDRESS: 5344 9th Street Zephyrhills, FL 33542	PHONE: (813)838-0735
	FAX: 1-(866)824-7894
	E-MAIL: erb@fbcplans.com
	WEBSITE: www.fbcplans.com
	C.O.A.: #29054

PROJECT	
HUDDLESTON	7321 CAYMAN CT
	PALMETTO, FL 34221

CONTRACTOR	
REPLACE MY CAGE	UNIT 12
6301 PORTER ROAD	SARASOTA, FL 34240

JOB NUMBER:	
26_0224_840_HUDDLESTON_REPLACMC	
DRAW DATE: 02/24/2026	
REVISION 1:	
REVISION 2:	
REVISION 3:	

DETAILS	
S-4	