

SOLOMON, JACQUELINE
15308 Valencia del Sol St, Wimauma,
Florida, 33598

GENERAL NOTES

1. DESIGN CRITERIA
FLORIDA BUILDING CODE (FBC), 8TH EDITION (2023/2024)
FLORIDA BUILDING CODE (FBC) AND ASSOCIATED CRITERIA FOR BUILDINGS AND OTHER STRUCTURES
ACI 318-19: BUILDING CODE REQUIREMENTS FOR STRUCTURAL CONCRETE.
ASTM STANDARDS AS SPECIFIED HEREIN.
ALUMINUM DESIGN MANUAL, 2020 EDITION (AA ADM-2020)
AA ASM 35-30: ALUMINUM STANDARDS AND DATA.
NATIONAL ELECTRICAL CODE (NEC), 2023 EDITION.

2. DESIGN LOADS
WIND SPEED (FBC CHAPTER 16): 140 MPH
ULTIMATE WIND SPEED (VULT) = 132 MPH PER ASCE 7-22, SECTION 26.5.1).
ALLOWABLE STRESS DESIGN WIND SPEED (VASD) = 103 MPH (VASD = VULT * 0.8).
RISK CATEGORY: 1 (URBAN OR SUBURBAN TERRAIN WITH OBSTRUCTIONS).
EXPOSURE CATEGORY: B (URBAN OR SUBURBAN TERRAIN WITH OBSTRUCTIONS).
DESIGN WIND PRESSURES INTERPOLATED FROM ASCE 7-22 AND REFERENCE TABLES FOR VULT = 140 MPH, EXPOSURE CATEGORY B.

WIND LOADS (MMFRS), BASED ON 140 MPH WIND SPEED AND EXPOSURE B:

- HORIZONTAL PRESSURE (WINDWARD): 24 PSF.
- HORIZONTAL PRESSURE (LEEWARD): 20 PSF.
- VERTICAL PRESSURE ON SCREEN SURFACE: 8 PSF.
- VERTICAL PRESSURE ON SOLID SURFACES: 25 PSF.

LOAD REDUCTION FACTORS:

- FOR 20X20X11" MESH SCREEN: 0.88 (MANUFACTURER DATA, ASCE 7-22 SECTION 30.5).
- FOR ALLOWABLE STRESS DESIGN PRESSURES: 0.6 (ASCE 7-22 SECTION 2.4).

3. CONTRACTOR RESPONSIBILITIES

- CONTRACTOR SHALL BE PERFORMED BY A LICENSED CONTRACTOR IN ACCORDANCE WITH APPLICABLE CODES, REGULATIONS, AND LOCAL ORDINANCES.
 - CONTRACTOR MUST FIELD-VERIFY ALL DIMENSIONS PRIOR TO FABRICATION OR CONSTRUCTION. WRITTEN DIMENSIONS SHALL GOVERN OVER SCALED DRAWINGS.
 - ANY DISCREPANCIES, ERRORS, OR OMISSIONS SHALL BE REPORTED TO THE ENGINEER IN WRITING WITHIN 10 DAYS OF PLAN RECEIPT AND PRIOR TO CONSTRUCTION.
 - CONTRACTOR SHALL PROVIDE ALL REQUIRED TEMPORARY SHORING, BRACING, AND SAFETY MEASURES DURING CONSTRUCTION.
 - CONTRACTOR SHALL PROTECT EXISTING STRUCTURES, UTILITIES, AND LANDSCAPING OUTSIDE THE SCOPE OF THIS PROJECT.
 - INSTALLATION PRACTICES MUST COMPLY WITH MANUFACTURER RECOMMENDATIONS, INCLUDING FLASHING AND WATERPROOFING DETAILS.
 - ALL UNDERGROUND UTILITIES SHALL BE LOCATED AND PROTECTED PRIOR TO EXCAVATION.
 - SHOP DRAWINGS AND MATERIAL CERTIFICATIONS SHALL BE PROVIDED UPON REQUEST.
 - CONTRACTOR SHALL MAINTAIN RECORDS OF INSPECTIONS AND TESTING.
 - FASTENER TORQUE AND EMBEDMENT TESTING RESULTS SHALL BE PROVIDED IF REQUESTED.
4. MATERIALS
- FOUNDATION
- ASSUMED SOIL BEARING CAPACITY: 2,000 PSF (VERIFY IN FIELD).
 - NOTIFY ENGINEER IF UNSUITABLE SOILS ARE ENCOUNTERED.
 - APPLY TERRACE TREATMENT AS REQUIRED BY FBC.
 - PLACE CONCRETE OVER VAPOR BARRIER WHERE APPLICABLE.
- CONCRETE
- MINIMUM COMPRESSIVE STRENGTH: 3,000 PSI @ 28 DAYS.
 - PORTLAND CEMENT: ASTM C150, TYPE I.



- AGGREGATE: 3/4" MAXIMUM, ASTM C33.
 - AIR ENTRAINMENT: 4-7%, ASTM C260.
 - WATER-REDUCING AGENT: ASTM C494.
 - WATER: CLEAN, POTABLE.
 - MINIMUM CURING TIME: 7 DAYS.
 - CURE CONCRETE FOR A MINIMUM OF 7 DAYS.
- STEEL REINFORCEMENT
- REINFORCING STEEL: ASTM A615, GRADE 60.
 - MINIMUM COVER FOR FOOTINGS: 2 INCHES.
 - LAP SPLICES: 40 TIMES BAR DIAMETER.
 - WELDED WIRE MESH PER ASTM A185.
 - FIBERMESH MAY BE SUBSTITUTED IF ASTM AND ACI REQUIREMENTS ARE MET.
- ALUMINUM
- STRUCTURAL ALUMINUM ALLOY: 6005-T5 MINIMUM.
 - DESIGN PER AA ADM-2020 SPECIFICATIONS.
 - MINIMUM WALL THICKNESS FOR EXTRUDED MEMBERS: 0.040 INCHES.
 - SELF-MATING BEAMS TO BE STITCHED WITH #12 SMS SCREWS:
 - 6" O.C. AT ENDS.
 - 18" O.C. ALONG SPANS.
 - KICK PLATES (FORMED PANELS) MINIMUM THICKNESS: 0.024 INCHES.
 - BACKBARS MESH SCREENS STANDARD UNLESS OTHERWISE APPROVED.
 - ALL ALUMINUM IN CONTACT WITH STEEL OR PRESSURE-TREATED LUMBER SHALL HAVE DIELECTRIC ISOLATION.
 - ALUMINUM ROOF SYSTEMS SHALL BE SELECTED PER MANUFACTURER SPAN TABLES CERTIFIED BY A LICENSED FLORIDA ENGINEER.
 - METAL STRUCTURES WITHIN 5 FEET OF POOLS SHALL BE BONDED PER NEC 680.26.

ALUMINUM EXTRUSION DIMENSIONS	
HOLLOW SECTIONS	
2 x 2	2" x 2" x 0.060"
2 x 3	2" x 3" x 0.060"
OPEN-BACK SECTIONS	
1 x 2	1" x 2" x 0.044"
SELF-MATING SECTIONS (SMB)	
2 x 4	2" x 4" x 0.044" x 0.100"
2 x 5CL	2" x 5" x 0.050" x 0.135"
2 x 6	2" x 6" x 0.050" x 0.120"
2 x 7	2" x 7" x 0.057" x 0.120"
2 x 8	2" x 8" x 0.072" x 0.224"
2 x 9	2" x 9" x 0.072" x 0.224"
2 x 10	2" x 10" x 0.092" x 0.314"
RECTUBE - 6005-T5 MIN.	
2 x 8	2" x 8" x 0.125" x 0.125"

FASTENERS

- ALL FASTENERS SHALL COMPLY WITH ASTM A193 FOR ZINC COATING.
- CONCRETE SCREWS: TAPCON, SIMPSON, HILTI, REDHEAD, OR APPROVED EQUAL.
- LAG BOLTS SHALL HAVE MINIMUM EMBEDMENT OF 8 TIMES BOLT DIAMETER.
- LAG BOLTS SHALL BE 1/2" (OR 5/8") SHALL BE USED FOR CONNECTIONS TO PRESSURE-TREATED WOOD.
- MINIMUM FASTENER SPACING:
- SMS: 3/4" CENTER-TO-CENTER, 1/2" EDGE DISTANCE.
- 1X2 MEMBERS TO MASONRY: 1/4" X 2-3/4" TAPSCREWS @ 18" O.C.
- 1X2 MEMBERS TO WOOD: #14 X 2-3/4" WOOD SCREWS @ 18" O.C.
- 1X2 MEMBERS TO ALUMINUM: #10 X 1-1/2" SMS OR TEK SCREWS @ 18" O.C.
- FOR "OPEN VIEW" OR "PICTURE WINDOW" ASSEMBLIES, REDUCE FASTENER SPACING TO 12" O.C.

5. ELECTRICAL

- ALL STRUCTURES WITHIN 5 FEET OF SWIMMING POOLS MUST BE BONDED IN ACCORDANCE WITH NEC 680.26.
- PROVIDE EQUIPOTENTIAL BONDING FOR ALL CONDUCTIVE ELEMENTS WITHIN POOL AREA.
- ALL ELECTRICAL WORK SHALL COMPLY WITH NEC 2023 EDITION AND LOCAL AMENDMENTS.


6. GENERAL REQUIREMENTS

- DIMENSIONS ARE NOMINAL UNLESS OTHERWISE NOTED.
- DIMENSIONAL TOLERANCES: ±1/8" UNLESS SPECIFIED.
- NOTES APPLY TO THE ENTIRE DRAWING SET UNLESS OTHERWISE INDICATED.
- REPORT ANY CONFLICTS IN DRAWINGS TO THE ENGINEER IMMEDIATELY.
- ALL DIMENSIONS AND LOCATIONS ARE TO FACE UNLESS OTHERWISE SPECIFIED.
- ENSURE SITE ACCESS FOR REQUIRED INSPECTIONS.
- FINAL CLEANUP IS REQUIRED PRIOR TO PROJECT CLOSEOUT.

NOTICE:

THE DATA IN THIS DOCUMENT INCORPORATES PROPRIETARY RIGHTS OF ACTIVE DESIGN LLC. ANY PARTY ACCEPTING THIS DOCUMENT DOES SO IN CONFIDENCE AND AGREES THAT IT SHALL NOT BE DUPLICATED IN WHOLE OR PART NOR DISCLOSED TO OTHERS WITHOUT THE CONSENT OF ACTIVE DESIGN LLC.

CONTRACTOR SHALL VERIFY ALL CONDITIONS ON JOB SITE & NOTIFY ENGINEER OF RECORD OF ANY VARIATIONS FROM DIMENSIONS SHOWN ON DRAWINGS BEFORE PROCEEDING WITH ANY CONSTRUCTION.

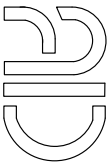

Active Design LLC
info@activedesigneng.com
(310) 963-4514

DATE:	SHEET:
3/27/2026	1
DRAWING TITLE:	NOTES
PROJECT NAME:	SOLOMON, JACQUELINE

HILLSBOROUGH COUNTY

PLANS REVIEWED FOR CODE COMPLIANCE

APPROVED

HC-BLD-26-0083270 4/22/2026

THIS SET OF PLANS MUST BE KEPT ON THE JOB SITE AT ALL TIMES
IT IS UNLAWFUL TO MAKE CHANGES OR ALTERATIONS WITHOUT APPROVAL
THE ISSUANCE OF THIS PERMIT SHALL NOT BE HELD TO PERMIT OR APPROVE THE VIOLATION OF ANY COUNTY, STATE OR FEDERAL LAW, CODE OR REGULATION

Building - Stephen

HILLSBOROUGH COUNTY

PLANS REVIEWED FOR CODE COMPLIANCE

APPROVED

HC-BLD-26-0083279 4/22/2026

THIS SET OF PLANS MUST BE KEPT ON THE JOB SITE AT ALL TIMES

IT IS UNLAWFUL TO MAKE CHANGES OR ALTERATIONS WITHOUT APPROVAL







THE ISSUANCE OF THIS PERMIT SHALL NOT BE HELD TO PERMIT OR APPROVE THE VIOLATION OF ANY COUNTY, STATE OR FEDERAL LAW, CODE OR REGULATION

REV	DESCRIPTION	DRAWN	REVIEWED	APPR.	DATE
1	INITIAL DESIGN	JDCV	AL	BC	3/27/2026



NOTE: Door location and framing are not structural and can be moved, as necessary, per contractor and owner approval.

LEGEND:
--- Indicated cable bracing. See details on sheet 3.

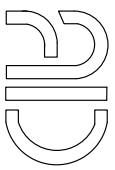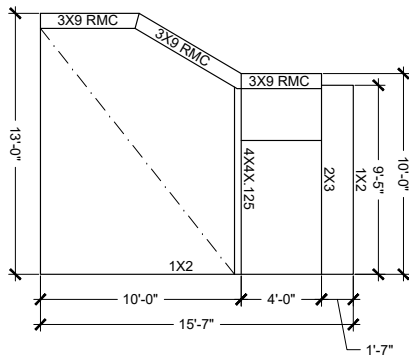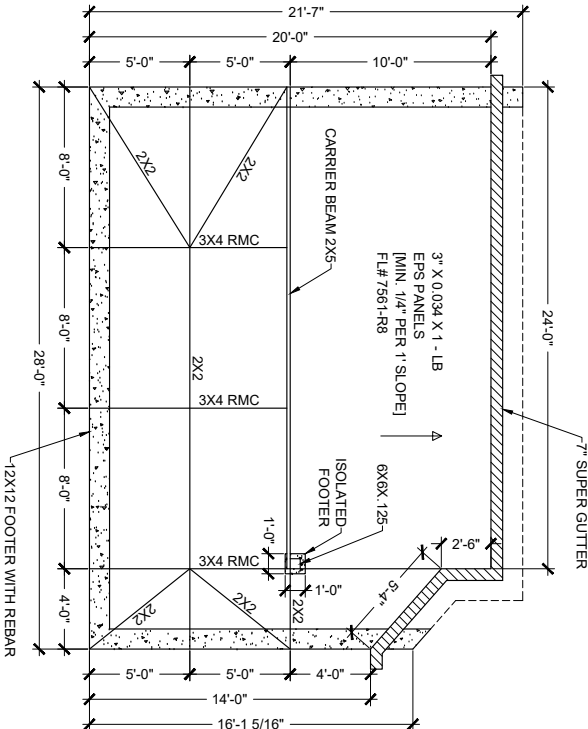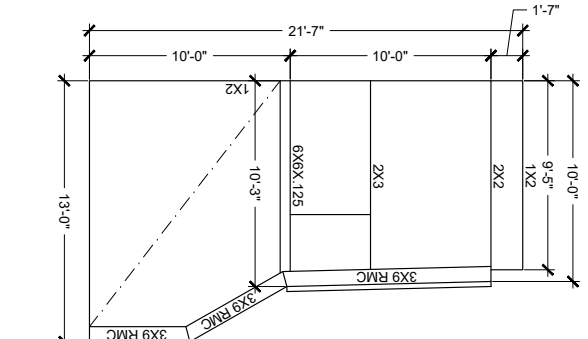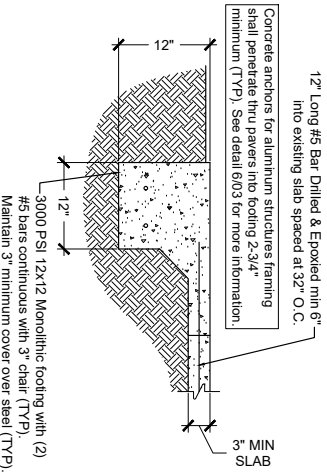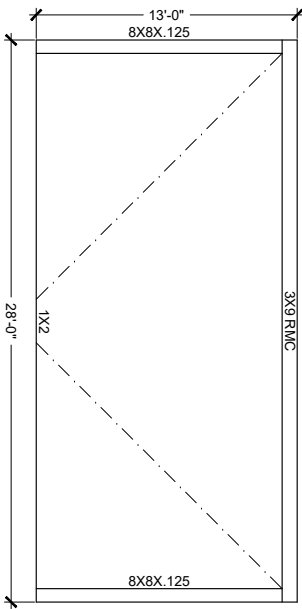

Active Design LLC
info@activedesigneng.com
(310) 963-4514

DATE:	SHEET:
3/27/2026	2
DRAWING TITLE:	STRUCTURAL DESIGN
PROJECT NAME:	SOLOMON, JACQUELINE



HILLSBOROUGH COUNTY

PLANS REVIEWED FOR CODE COMPLIANCE

APPROVED

HC-BLD-26-0083279 4/22/2026

THIS SET OF PLANS MUST BE KEPT ON THE JOB SITE AT ALL TIMES


IT IS UNLAWFUL TO MAKE CHANGES OR ALTERATIONS WITHOUT APPROVAL

THE ISSUANCE OF THIS PERMIT SHALL NOT BE HELD TO PERMIT OR APPROVE THE VIOLATION OF ANY COUNTY, STATE OR FEDERAL LAW, CODE OR REGULATION


REV	DESCRIPTION	DRAWN	REVIEWED	APPR.	DATE
1	INITIAL DESIGN	JDEV	AL	BC	3/27/2026

Column To Beam Connection

SCALE: 3" = 1'-0"

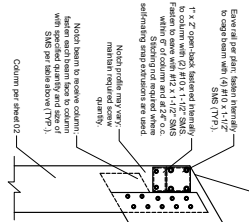

BEAM	SPACING
2X4	4'-8 1/2"
2X6	4'-8 1/2"
2X8	4'-8 1/2"
2X10	6'-8 1/2"
2X12	6'-8 1/2"
3X6	4'-8 1/2"
3X8	4'-8 1/2"
3X10	6'-8 1/2"
3X12	6'-8 1/2"
4X10	6'-8 1/2"

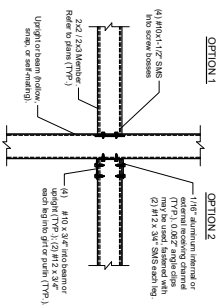


Beam Post to Girt/Purlin Connection

SCALE: 3" = 1'-0"


Cable to Foundation Connection

SCALE: 3" = 1'-0"

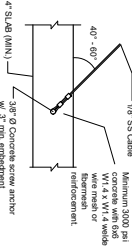


Roof Brace Connection

SCALE: 3" = 1'-0"

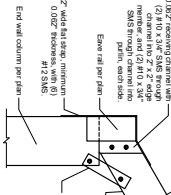

Column To FND Connection For 2x4 or Larger


SCALE: 3" = 1'-0"

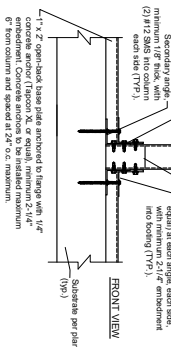

Beam to Gutter Connection

SCALE: 3" = 1'-0"

1. Facia to be maintained to within 1/4\"/>
2. 7\"/>

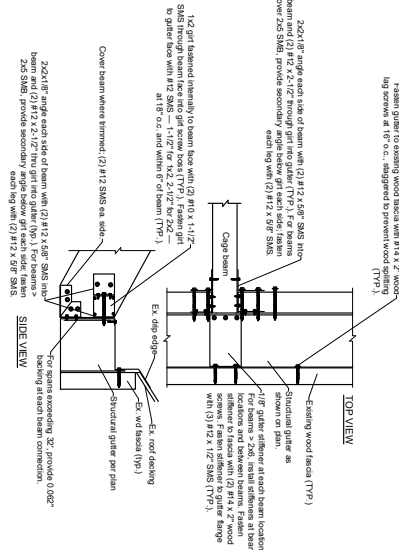

BEAM SIZE	QUANTITY OF #12 SMS PER BEAM FACE/SIDE/TOTAL FOR CONNECTION.	QUANTITY OF #14 SMS PER BEAM FACE/SIDE/TOTAL FOR CONNECTION.
2X4 SMB	9/18/36	
2X6 SMB	9/18/36	
2X8 SMB	10/20/40	12/24/48
2X10 SMB		12/24/48
2X12 SMB		13/26/52
3X4 RMC	9/18/36	
3X6 RMC	9/18/36	
3X8 RMC	10/20/40	12/24/48
3X10 RMC		12/24/48
3X12 RMC		13/26/52
4X10 RMC		13/26/52

Active Design LLC

info@activedesigneng.com

(310) 963-4514

DATE:	SHEET:
3/27/2026	3
DRAWING TITLE:	DETAILS 1
PROJECT NAME:	SOLOMON, JACQUELINE

HILLSBOROUGH COUNTY

PLANS REVIEWED FOR CODE COMPLIANCE

APPROVED

HC-BLD-26-0083279 4/22/2026

THIS SET OF PLANS MUST BE KEPT ON THE JOB SITE AT ALL TIMES

IT IS UNLAWFUL TO MAKE CHANGES OR ALTERATIONS WITHOUT APPROVAL

THE ISSUANCE OF THIS PERMIT SHALL NOT BE HELD TO PERMIT OR APPROVE THE VIOLATION OF ANY COUNTY, STATE OR FEDERAL LAW, CODE OR REGULATION

1

INITIAL DESIGN

REVISION

DESCRIPTION

DRAWN

REVIEWED

APPR.

DATE


JDCV

AL

BC


3/27/2026

Beam Splice Detail
SCALE: 3" = 1'-0"

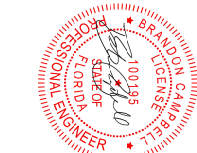


- NOTE
- Beam splice length to be 2x beam height.
 - Locate beam splice at 1/3 points.
 - Provide minimum 1" center in beam to reduce self-weight deflection.

FASTENER QUANTITY TABLE		
BEAM SIZE	FASTENER SIZE	QUANTITY PER FACE/SIDE/TOTAL
2X4 SMB	#12	6 / 12 / 24
2X6 SMB	#12	10 / 20 / 40
2X8 SMB	#12	12 / 24 / 48
2X8 SMB	#14	12 / 24 / 48
2X10 SMB	#14	18 / 36 / 72
3X4 RMC	#12	6 / 12 / 24
3X6 RMC	#12	10 / 20 / 40
3X7 RMC	#12	12 / 24 / 48
3X8 RMC	#14	18 / 36 / 72
3X10 RMC	#14	18 / 36 / 72
4X10 RMC	#14	18 / 36 / 72

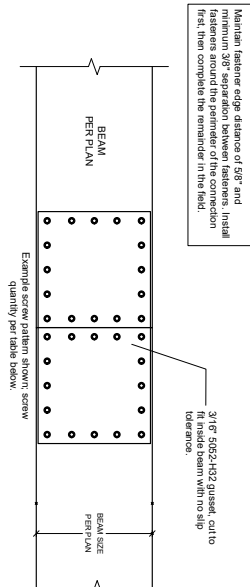


Beam Under Overhang Detail
SCALE: 3" = 1'-0"


1. Fascia shall be secured to rafter tail with (1) 1/4" Ø x 4" lag screw.
2. A 7" gutter may be used, provided strap length is increased by 2".

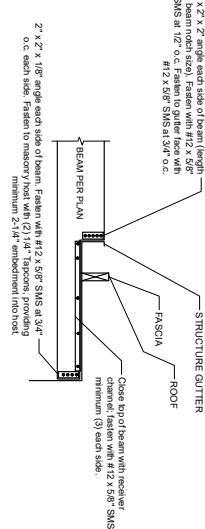


Beam to Edge Beam Detail
SCALE: 1-1/2" = 1'-0"

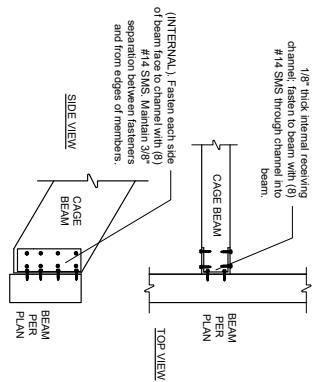


Beam to Column Connection
SCALE: 3" = 1'-0"

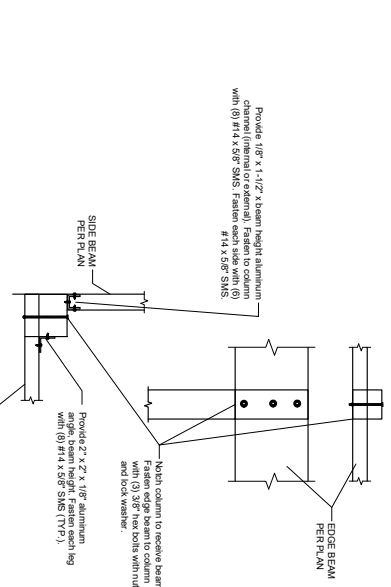


Purlin to Edge Beam Detail
SCALE: 3" = 1'-0"

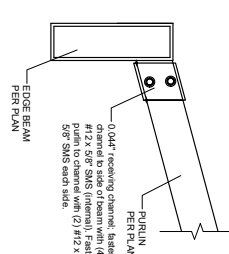

Post Base Connection
SCALE: 3" = 1'-0"

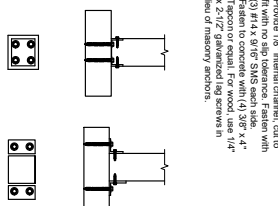




K-Brace Detail
SCALE: 2" = 1'-0"

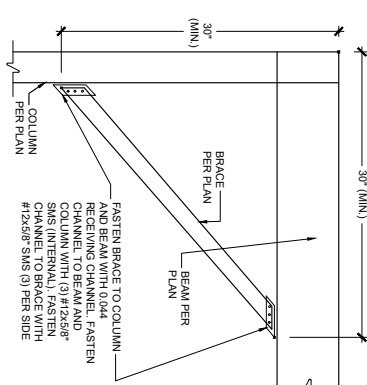

Active Design LLC
info@activedesigneng.com
(310) 963-4514

DATE:	SHEET:
3/27/2026	4
DRAWING TITLE:	DETAILS CONT.
PROJECT NAME:	SOLOMON, JACQUELINE

 Active Design LLC info@activedesigneng.com (310) 963-4514	
DATE: 3/27/2026	SHEET: 5
DRAWING TITLE: DETAILS CONT.	
PROJECT NAME: SOLOMON, JACQUELINE	

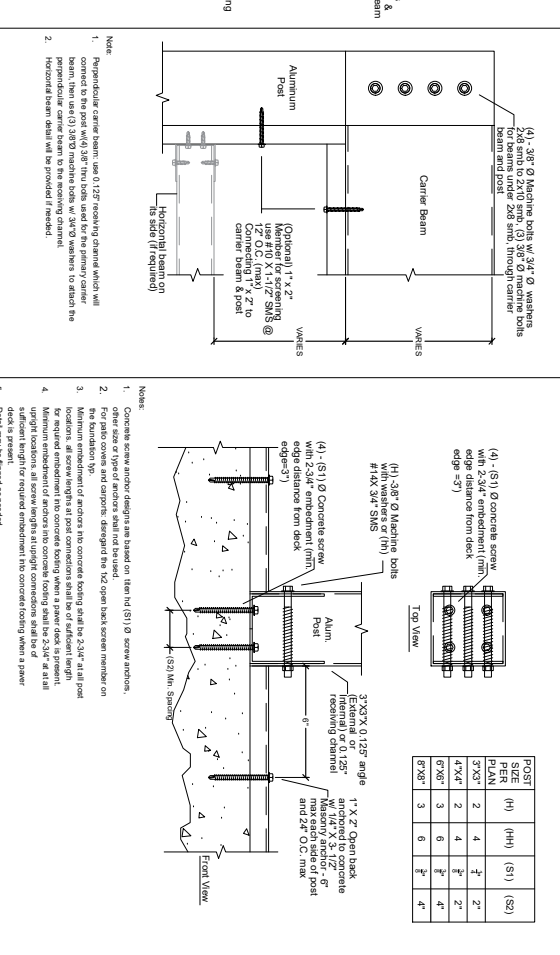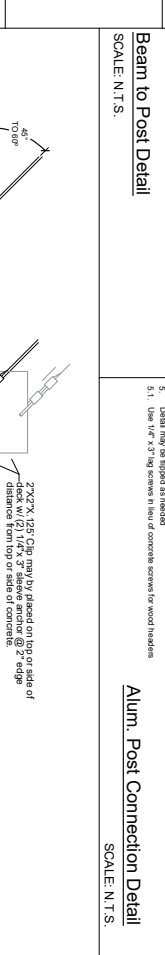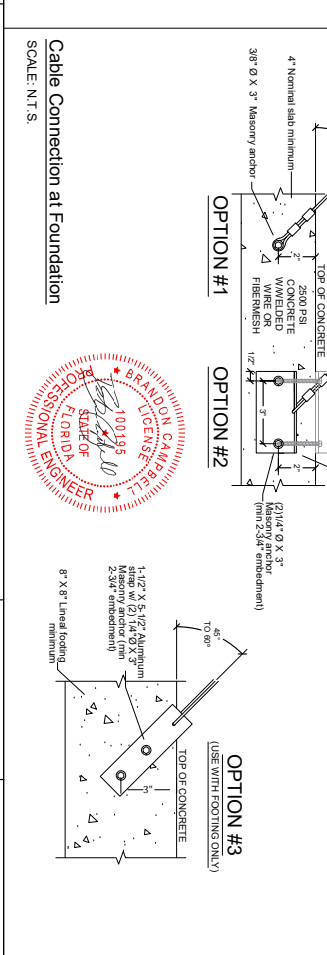

HILLSBOROUGH COUNTY

PLANS REVIEWED FOR CODE COMPLIANCE

APPROVED

HC-BLD-26-0083279 4/22/2026


THIS SET OF PLANS MUST BE KEPT ON THE JOB SITE AT ALL TIMES

IT IS UNLAWFUL TO MAKE CHANGES OR ALTERATIONS WITHOUT APPROVAL


THE ISSUANCE OF THIS PERMIT SHALL NOT BE HELD TO PERMIT OR APPROVE THE VIOLATION OF ANY COUNTY, STATE OR FEDERAL LAW, CODE OR REGULATION

REV	DESCRIPTION	DRAWN	REVIEWED	APPR.	DATE	NOTICE:	DATE:	SHEET:
1	INITIAL DESIGN	JDCV	AL	BC	3/27/2026	THE DATA IN THIS DOCUMENT INCORPORATES PROPRIETARY RIGHTS OF ACTIVE DESIGNS LLC. ANY PARTY ACCEPTING THIS DOCUMENT DOES SO IN CONFIDENCE AND AGREES THAT IT SHALL NOT BE DUPLICATED IN WHOLE OR PART NOR DISCLOSED TO OTHERS WITHOUT THE CONSENT OF ACTIVE DESIGNS LLC. CONTRACTOR SHALL VERIFY ALL CONDITIONS ON JOB SITE & NOTIFY ENGINEER OF RECORD OF ANY VARIATIONS FROM DIMENSIONS SHOWN ON DRAWINGS BEFORE PROCEEDING WITH ANY CONSTRUCTION.	3/27/2026	6
PROJECT NAME: SOLOMON, JACQUELINE							DRAWING TITLE: DETAILS CONT.	


ULTIMATE VIEW UPRIGHT TO BEAM WELD GUSSET MATERIAL

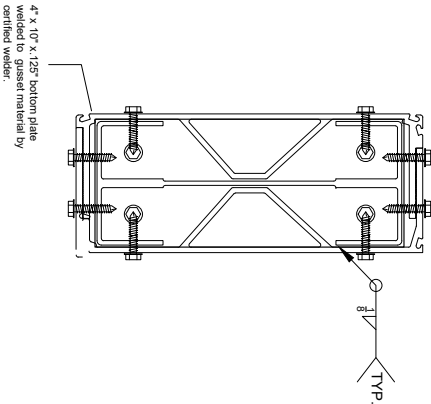



ULTIMATE VIEW BASE MATERIAL

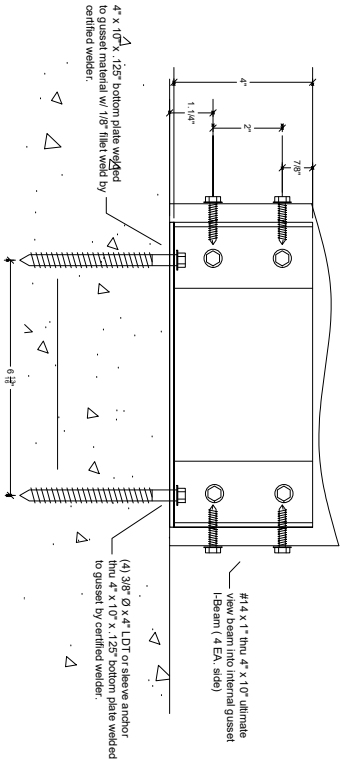

ULTIMATE VIEW GUSSET MATERIAL

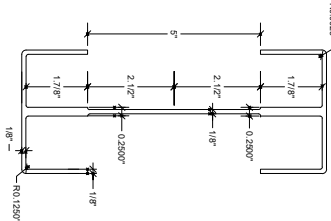


ULTIMATE VIEW UPRIGHT TO BEAM GUSSET MATERIAL

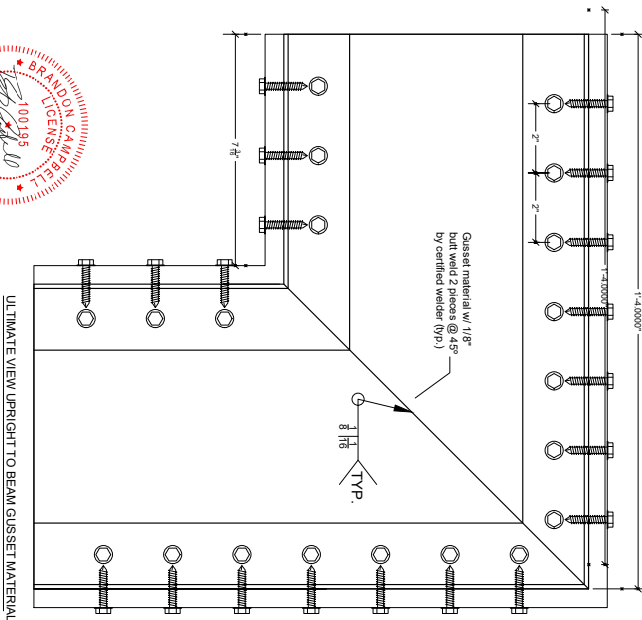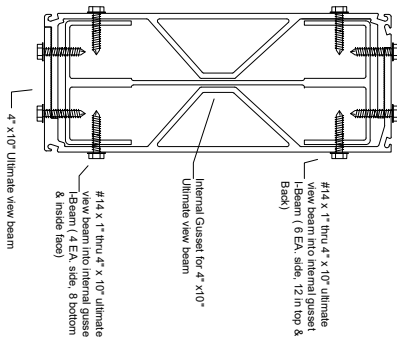


- Note:
- Horizontal splice shall be done similar to corner splice w/ 24" I-beam insert w/ (5) #14 xt SMS EA, section as shown above.
 - Angular splice shall also be done similar as above.
 - Beam continuation use base plate on back side of post & attach with (4) #16X 2" SMS.

Active Design LLC
info@activedesigneng.com
(310) 963-4514

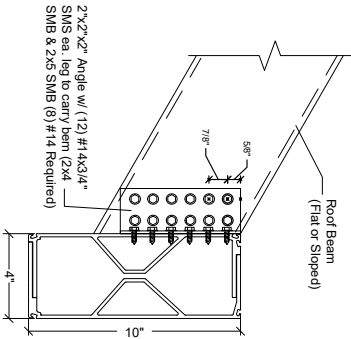


Roof Beam to Carrier Beam Connection Detail

SCALE: N.T.S.

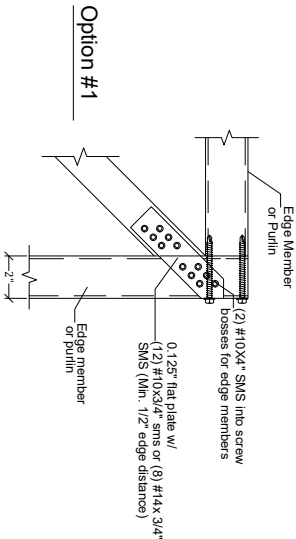

Option #1


Both ends similar

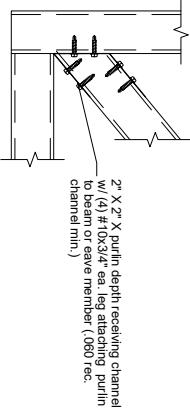

Option #2

Roof Bracing Connection Detail

SCALE: N.T.S.

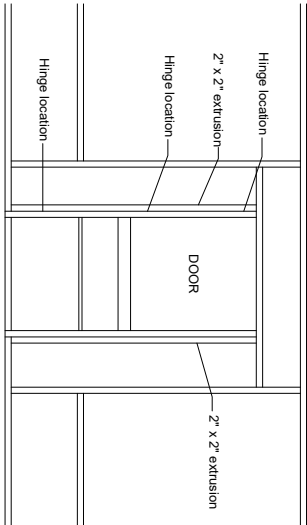

Typical Screen Door Connection Detail

SCALE: N.T.S.

- Notes:
1. Hinges shall be attached to structure w/ (3) #10 x 5/8" SMS minimum.
 2. Door shall be attached to enclosure w/ (2) hinges minimum.
 3. Hinges shall be attached to door with (3) #10 x 5/8" SMS, fasten a 1" x 2" x 0.044" to upright w/ #12 x 1" SMS @ 12" O.C. and within 3" from end of the upright (if applicable).

REV	DESCRIPTION	DRAWN	REVIEWED	APPR.	DATE
1	INITIAL DESIGN	JDCV	AL	BC	3/27/2026

NOTICE:

THE DATA IN THIS DOCUMENT INCORPORATES PROPRIETARY RIGHTS OF ACTIVE DESIGNS LLC. ANY PARTY ACCEPTING THIS DOCUMENT DOES SO IN CONFIDENCE AND AGREES THAT IT SHALL NOT BE DUPLICATED IN WHOLE OR PART NOR DISCLOSED TO OTHERS WITHOUT THE CONSENT OF ACTIVE DESIGNS LLC. CONTRACTOR SHALL VERIFY ALL CONDITIONS ON JOB SITE & NOTIFY ENGINEER OF RECORD OF ANY VARIATIONS FROM DIMENSIONS SHOWN IN THESE DRAWINGS BEFORE PROCEEDING WITH ANY CONSTRUCTION.



Active Design LLC
info@activedesigneng.com
(310) 963-4514

DATE:	SHEET:
3/27/2026	7
DRAWING TITLE:	DETAILS CONT.
PROJECT NAME:	SOLOMON, JACQUELINE

HILLSBOROUGH COUNTY
PLANS REVIEWED FOR CODE COMPLIANCE
APPROVED
HC-BLD-26-0083279 4/22/2026
THIS SET OF PLANS MUST BE KEPT ON THE JOB SITE AT ALL TIMES
IT IS UNLAWFUL TO MAKE CHANGES OR ALTERATIONS WITHOUT APPROVAL
THE ISSUANCE OF THIS PERMIT SHALL NOT BE HELD TO PERMIT OR APPROVE THE VIOLATION OF ANY COUNTY, STATE OR FEDERAL LAW, CODE OR REGULATION

HILLSBOROUGH COUNTY
PLAT 133, PAGES 034 THROUGH 067, OF THE PUBLIC RECORDS OF HILLSBOROUGH COUNTY, FLORIDA.
APPROVED
THIS SET OF PLANS AND SPECIFICATIONS IS KEPT ON THE JOB SITE AT ALL TIMES.
THE ISSUANCE OF THIS PERMIT SHALL NOT BE HELD TO BE A GUARANTEE OF THE ACCURACY OF THE INFORMATION CONTAINED HEREON.

AS BUILT SURVEY (FINAL)
WITH SELECTIVE SPOT ELEVATIONS

LOT 296
VALENCIA DEL SOL PHASE 1
HILLSBOROUGH COUNTY, FLORIDA.

LEGEND:
E00.00 = EXISTING GRADE

PREPARED FOR & CERTIFIED TO:
NOVA TITLE CO.
WFG NATIONAL TITLE INSURANCE CO.
GLFINANCIAL SERVICES, LLC
CAREY GORDON SOLOMON
JACQUELINE A. SOLOMON

SEC. 32, TWP. 31 S, RNG. 20 E.

BEARING BASIS:
WEST BOUNDARY OF SUBJECT PLAT BEING N 00°21'46" E

N
SCALE: 1" = 30'

THIS SURVEY IS SUBJECT TO ANY FACTS THAT MAY BE DISCLOSED BY A FULL AND ACCURATE TITLE SEARCH. ALSO SUBJECT TO SETBACKS, EASEMENTS AND RESTRICTIONS OF RECORD.

UNDERGROUND FOOTER, STEM WALL, AND UNDERGROUND UTILITIES ARE NOT LOCATED OR SHOWN.


DO NOT SCALE THIS PRINT. DIMENSIONS AND NOTES TAKE PREFERENCE.

STRUCTURE TIES SHOWN HEREON DENOTES MEASUREMENT FROM FORM BOARDS/FOUNDATION TO PROPERTY LINE.

PURPOSE OF SURVEY: TO OBTAIN HORIZONTAL AND/OR VERTICAL DIMENSIONAL DATA TO SHOW CONSTRUCTION IMPROVEMENTS.

* = 10' PUBLIC UTILITY EASEMENT

VALENCIA DEL SOL STREET
(PRIVATE R/W WIDTH VARIES) (TRACT "A")
(PUBLIC ACCESS & UTILITIES EASEMENT)

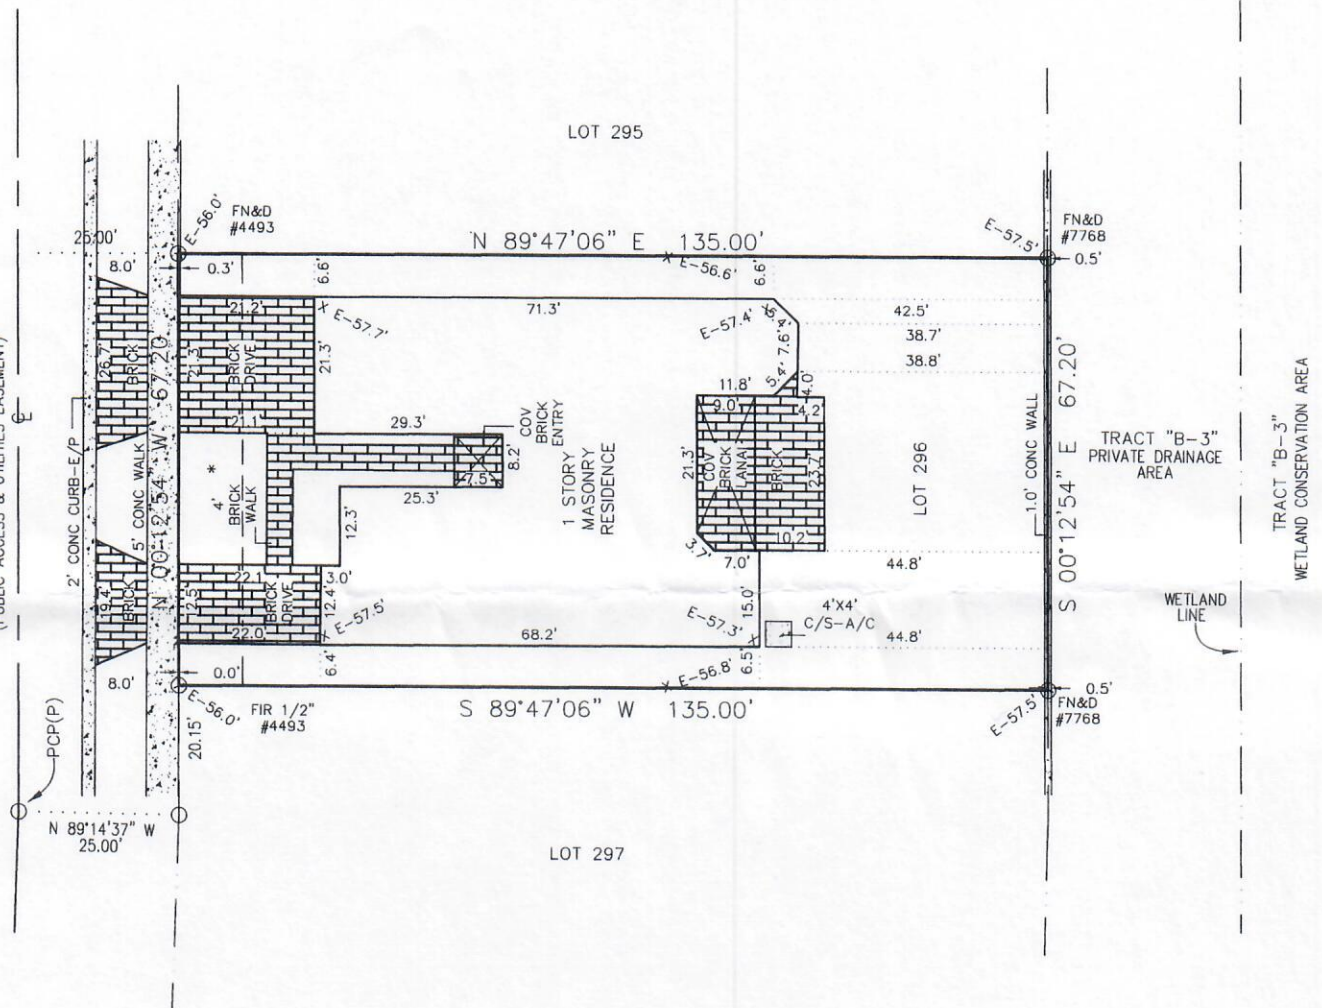

DESCRIPTION:

LOT 296, MAP OR PLAT ENTITLED "VALENCIA DEL SOL PHASE 1", AS RECORDED IN PLAT BOOK 133, PAGES 034 THROUGH 067, OF THE PUBLIC RECORDS OF HILLSBOROUGH COUNTY, FLORIDA.

LOWEST FLOOR ELEVATIONS:
LIVING AREA: 58.11'
GARAGE AREA: 57.66'
ELEVATIONS REFERENCED TO
NORTH AMERICAN VERTICAL
DATUM OF 1988. MEAN SEA
LEVEL= 00.00 FT.

APPARENT FLOOD HAZARD ZONE: "X" COMMUNITY PANEL NO. 12057C 0680 H EFFECTIVE DATE: 8/28/08

LEGEND:
(C)= CALCULATED DATA, (D)= DEED DATA, (M)= MEASURED DATA, (P)= PLAT DATA, CL= CENTERLINE, A/C= AIR CONDITIONER, B/C= BACK OF CURB, C/S= CONCRETE SLAB, CH= CHORD, CHB= CHORD BEARING, CLF= CHAIN LINK FENCE, CONC= CONCRETE, COV.= COVERED, E/P= EDGE OF PAVEMENT, ESM=T= EASEMENT, F/C= FENCE CORNER, FCM= FOUND CONCRETE MONUMENT, FIP= FOUND IRON PIPE, FIR= FOUND IRON ROD, FN&D= FOUND NAIL & DISK, FPP= FOUND PINCHED PIPE, LFE= LOWEST FLOOR ELEVATION, MAS.= MASONRY, OR= OFFICIAL RECORD BOOK, PB= PLAT BOOK, PCP= PERMANENT CONTROL POINT, PRM= PERMANENT REFERENCE MONUMENT, R/W= RIGHT OF WAY, R= RADIUS, SIR= SET 1/2" IRON ROD & CAP No. 4493, SN&D= SET NAIL & DISK No. 4493, TBM= TEMPORARY BENCHMARK, U/P= UTILITY POLE, W/F= WOOD FENCE

JOHN R. BEACH & ASSOCIATES, INC.
SURVEYORS AND MAPPERS
911 WEST ST. PETERSBURG DRIVE
OLDSMAR, FLORIDA 34677
(813) 854-1276 FAX (813) 855-8370

Drawn By:
SMS
Checked By:
JRB
Scale:
1"=30'

I HEREBY CERTIFY THAT THIS SURVEY WAS MADE UNDER MY RESPONSIBLE CHARGE AND MEETS THE APPLICABLE STANDARDS OF PRACTICE FOR SURVEYS AS SET FORTH BY THE FLORIDA BOARD OF LAND SURVEYORS IN CHAPTER 5J-17.051 THROUGH 5J-17.053, FLORIDA ADMINISTRATIVE CODE, PURSUANT TO SECTION 472.027 FLORIDA STATE STATUTES.

NOT VALID WITHOUT ORIGINAL SIGNATURE AND SEAL OF A FLORIDA LICENSED SURVEYOR AND MAPPER

Date: FINAL 08/16/2021 JT

SIGNATURE
DATE

Revisions: FORM BOARD TIE IN 12/29/20 JMC, FOUNDATION TIE IN 01/13/2021 RTM

JOHN R. BEACH
FLORIDA REG. LAND SURVEYOR No. 2984
JOHN R. McDONALD
PROFESSIONAL SURVEYOR & MAPPER No. 6986

LB#4493